都市計画情報図

この用紙には、複数の不正防止処理を施してあります。



■区域区分	市街化区域
■用途地域	第1種低層住居専用地域
建ぺい率	40%
容積率	80%
■地域地区	
防火・準防火地域	－
建築基準法第22条区域	○
高度利用地区	－
景観地区	－
臨港地区	－
風致地区	－
特別緑地保全地区	－
生産緑地地区	－
■都市施設	
道路(名称・最終告示番号・告示日・幅員)	－
都市計画道路整備状況(問合せ先)	－
都市計画道路整備状況	－
都市計画道路整備路線名	－
都市高速鉄道	－
駐車場(駐輪場)	－
公園(名称・最終告示番号・告示日)	－
緑地	－
墓園	－
汚物処理場	－
ごみ焼却場	－
その他供給施設又は処理施設	－
河川	－
市場	－
火葬場	－
■市街地開発事業	
土地区画整理事業	－
工業団地造成事業	－
市街地再開発事業	－
■土地区画整理促進区域	－
■地区計画	－

地域地区
- 都市計画区域
- 市街化区域
- 市街化調整区域
- 高度利用地区
- 風致地区
- 臨港地区
- 特別緑地保全地区
- 生産緑地地区
- 景観地区
- 防火地域
- 準防火地域

建築基準法第22条区域
- 建築基準法第22条区域

用途地域
- 第1種低層住居専用地域
- 第2種低層住居専用地域
- 第1種中高層住居専用地域
- 第2種中高層住居専用地域
- 第1種住居地域
- 第2種住居地域
- 準住居地域
- 近隣商業地域
- 商業地域
- 準工業地域
- 工業地域
- 工業専用地域

促進地域
- 土地区画整理促進地域

公共空地
- 公園
- 緑地
- 墓園

地図計画等
- 地区計画

都市計画施設
- 道路：整備済
- 道路：要確認
- 道路：未整備
- 駐輪場
- 公共下水道区域
- ごみ焼却場
- 汚物処理場
- その他供給施設・処理施設
- 河川

その他
- 市場
- 火葬場
- 市街地再開発事業
- 土地区画整理事業
- 工業団地造成事業

- 上表内容の欄は、地図上中心の都市計画情報の内容を表示しています。
- 表示に利用している地図は土地の境界を示すものではありません。
- 本図は、都市計画図(1/2500)を基に電子閲覧用に加工したものであり、地図作成上の誤差を含んでいます。
- 本図の使用によって発生する直接または間接の損失、損害及び障害等について一切責任を負いません。
- 本図に記載の用途スタンプは、掲載の都合により用途スタンプ位置と実際の用途地域が異なる場合があるため、用途地域の凡例と合わせてご確認ください。
- 本図は本市の都市計画情報の証明書ではありません。

20260903-窓口02-0003-01

最終更新時点：2026年4月1日

この都市計画情報図は、藤沢市が作成し、縦覧しているものの写しに相違ありません。


2026年（令和8年）9月3日

藤沢市長　鈴　木　恒　夫

この用紙には、複数の不正防止処理を施してあります。

この用紙には、複数の不正防止処理を施してあります。

まちづくり情報図

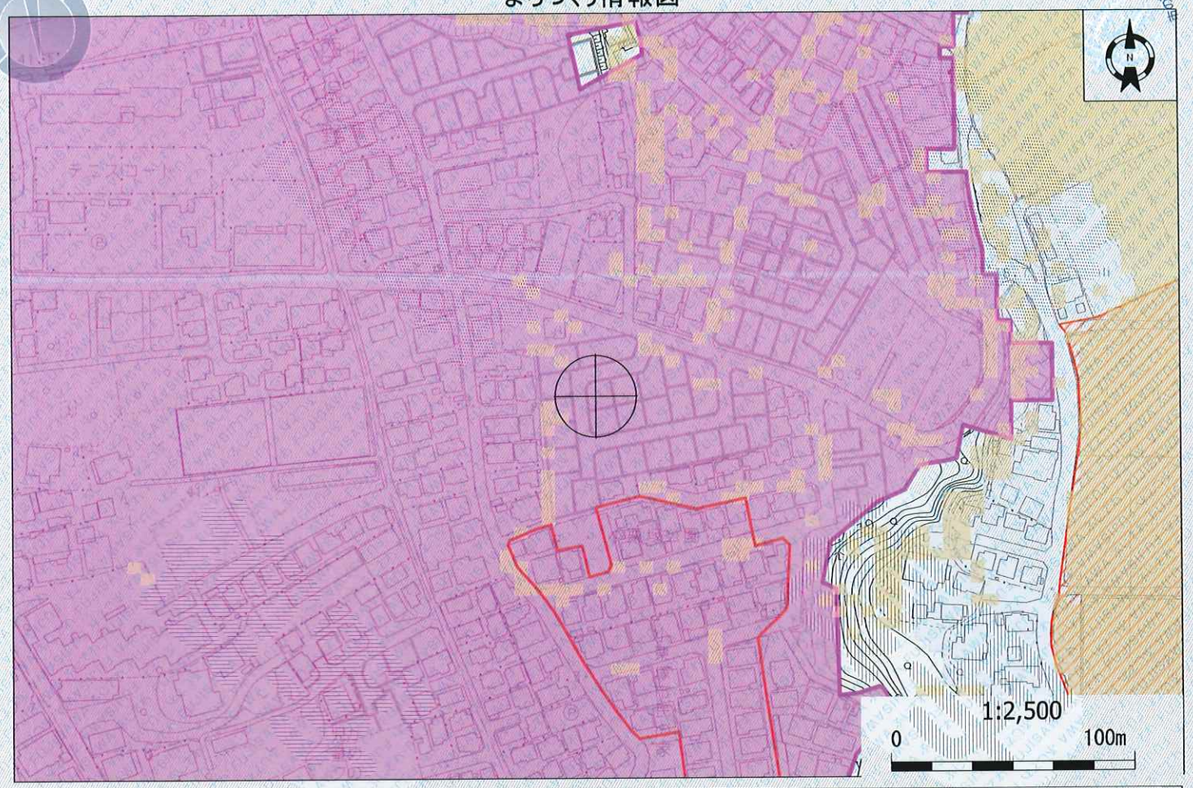

■開発業務課	☎0466-50-3538
小田急通り線	–
■産業労働課	☎0466-50-3530
街づくり協定　※一部地区で更新中のため、最新情報は産業労働課HPをご確認ください。	–
■街なみ景観課	☎0466-50-3508
景観形成地区	–
景観計画	市全域
街なみ継承地区	–
住民協定（内容等は各協定の運営委員会へ）	–
■建築指導課	☎0466-50-3539
建築協定同意範囲	–
片瀬山自治会　土地・建物にかかわる申し合わせ事項	–
建築基準法施行令第131条の2の規定に基づき指定をする街区	–
■都市計画課	☎0466-50-3537
都市景観の指導	–
都市機能誘導区域	区域外
居住誘導区域	区域内
■防災政策課・神奈川県藤沢土木事務所	
土砂災害警戒区域	担当課/HP（神奈川県土砂災害情報ポータル）でご確認ください。
急傾斜地崩壊危険区域	担当課/HP（神奈川県土砂災害情報ポータル）でご確認ください。
■道路整備課	☎0466-50-3547
道路改良事業計画	–
■藤沢駅周辺地区整備担当	☎0466-50-3552
藤沢駅前街区まちづくりガイドライン対象区域	–
■みどり保全課	☎0466-50-8252
川名緑地区域	–
藤沢市緑の保全及び緑化の推進に関する条例	○
■防災政策課	☎0466-50-8380
洪水浸水想定区域	–
津波災害警戒区域	–
家屋倒壊等氾濫想定区域	–
高潮浸水想定区域	–
■下水道計画業務課	☎0466-50-8246
内水浸水想定区域	–
■住まい暮らし政策課	☎0466-50-3541
再生可能エネルギー利用促進区域	○

- 【旧】宅地造成工事規制区域
- 街づくり協定
- 景観形成地区
- 景観計画
- 街なみ継承地区
- 建築協定同意範囲
- 片瀬山自治会連絡会（土地・建物にかかわる申し合わせ事項）
- 都市景観の指導
- 小田急通り線
- 道路改良事業計画
- 建築基準法施行令第131条の2の規定に基づき指定する街区
- 都市機能誘導区域
- 居住誘導区域
- 藤沢駅前街区まちづくりガイドライン対象区域
- 川名緑地区域
- 家屋倒壊等氾濫想定区域
- 高潮浸水想定区域
- 洪水浸水想定区域
- 津波災害警戒区域
- 内水浸水想定区域
- 再生可能エネルギー利用促進区域

- 上表内容の欄は、地図上中心のまちづくり情報の内容を表示しています。
- 表示に利用している地図は土地の境界を示すものではありません。
- 本図は、都市計画図(1/2500)を基に電子閲覧用に加工したものであり、地図作成上の誤差を含んでいます。
- 本図の使用によって発生する直接または間接の損失、損害及び障害等について一切責任を負いません。
- 埋蔵文化財包蔵地については、郷土歴史課へご相談ください。
- 鵠沼地区における住民協定の取り組みについては、街なみ景観課で周知しています。
- 本図は本市のまちづくり情報の証明書ではありません。
- 宅地造成等工事規制区域については、神奈川県砂防課厚木南駐在事務所へご相談ください。

立地適正化計画 防災指針について

神奈川県土砂災害情報ポータル

このまちづくり情報図は、藤沢市が作成し、縦覧しているものの写しに相違ありません。

2026年（令和8年）9月3日

藤沢市長　鈴　木　恒　夫

最終更新時点：2026年4月1日

20260903-窓口02-0003-02

この用紙には、複数の不正防止処理を施してあります。

開発登録簿

（調書）

市名	藤沢市	番号	H29-023

開発許可	許可番号	指令開業第29号-124		許可年月日	2017年(平成29年)08月17日
	許可を受けた者	住所	藤沢市湘南台一丁目1番地の21		
		氏名	株式会社一平不動産 代表取締役　廣木　正雄		
承継	承継番号			承継年月日	
	承継を受けた者	住所			
		氏名			
当初許可	開発区域に含まれる地域の名称	藤沢市西俣野字北窪306-1の一部、307-1の一部、307-4、307-5の一部			
	区域・地域等	市街化区域　第一種低層住居専用地域			
	都市計画法第41条の規定による制限の内容				
	工事施工者	住所	藤沢市湘南台一丁目1番地の21		
		氏名	株式会社一平不動産 代表取締役　廣木　正雄		
	開発区域の総面積(㎡)	工区数	工区面積	予定建築物の用途	専用住宅（11区画）
	2,189.76				
備考		これは、開発登録簿の写であることを証する。 2026年（令和8年）9月 3日 藤沢市長　鈴 木 恒 夫			

備考　都市計画法第41条第2項ただし書（同法第34の2第2項及び同法35条の2項第4項において準用する場合を含む。）若しくは第42第1項ただし書の規定による許可または同条第2項の規定による協議を行った場合には、許可年月日、許可番号を備考欄に記入すること。

整理番号　20260903-窓口02-0003-04

この用紙には、複数の不正防止処理を施してあります。

この用紙には、複数の不正防止処理を施してあります。

（調書）

変更許可	変更許可番号	変更許可年月日	変更の内容
	指令開業第29号-237	2017年(平成29年)11月24日	擁壁の長さの変更

変更の届出	変更届出年月日	届出の内容

工事完了検査	工区号			概要（公共施設のみの場合はその名称）
	検査済証	番号	開業第316号	
		交付年月日	2018年(平成30年)01月11日	
	完了公告	番号	藤沢市公告第275号	
		公告年月日	2018年(平成30年)01月12日	
	工区号			概要（公共施設のみの場合はその名称）
	検査済証	番号		
		交付年月日		
	完了公告	番号		
		公告年月日		
	工区号			概要（公共施設のみの場合はその名称）
	検査済証	番号		
		交付年月日		
	完了公告	番号		
		公告年月日		

整理番号　20260903-窓口02-0003-04

この用紙には、複数の不正防止処理を施してあります。

この用紙には、複数の不正防止処理を施してあります。

管理番号　：H29確申建築藤沢市001775

建築確認台帳記載事項証明書

【1.建築主】
(1)　【イ.氏名】　株式会社　一平不動産　代表取締役　廣木　正雄
　　【ロ.住所】　神奈川県藤沢市湘南台1-1-21

【2.敷地の位置】
　　【イ.地名地番】　神奈川県藤沢市西俣野字北窪306-12

【3.建築物の概要】
　　【イ.主要用途】　一戸建ての住宅
　　【ロ.工事種別】　新築
　　【ハ.敷地面積】　121.47㎡
　　【ニ.建築面積】　53.82㎡
　　【ホ.延べ面積】　95.23㎡
　　【ヘ.構造】　木造
　　【ト.階数】　地上　2　階　　地下　　階

【4.建築確認】
　　【イ.確認済証交付者】　一般財団法人神奈川県建築安全協会
　　【ロ.確認済証番号】　第 17KAK建確05090 号
　　【ハ.交付年月日】　平成30年1月23日

【5.完了検査】
　　【イ.検査済証交付者】　一般財団法人神奈川県建築安全協会
　　【ロ.検査済証番号】　第　18KAK建済00602　号
　　【ハ.交付年月日】　平成30年5月14日

上記の事項は藤沢市で保管する記載事項証明と相違ないことを証明します。

2026年(令和8年) 9月 3日

藤 沢 市 長　鈴 木 恒 夫

整理番号 20260903-窓口02-0003-05　　1/1

この用紙には、複数の不正防止処理を施してあります。

この用紙には、複数の不正防止処理を施してあります。

1775

第三号様式（第一条の三、第三条、第三条の三、第三条の四、第三条の七、第三条の十、第六条の三、十一条の四関係）（Ａ４）

※受付欄		
	受付番号	第１７ＫＡＫ建確０５０９０号
	受付日	３０．１．１８
	確認済証番号	第１７ＫＡＫ建確０５０９０号
	発行日	３０．１．２３

H29

建築計画概要書（第一面）

建築主等の概要

【１．建築主】
【イ．氏名のﾌﾘｶﾞﾅ】　ｶﾌﾞｼｷｶﾞｲｼｬ ｲｯﾍﾟｲﾌﾄﾞｳｻﾝ ﾀﾞｲﾋｮｳﾄﾘｼﾏﾘﾔｸ ﾋﾛｷ ﾏｻｵ
【ロ．氏名】　株式会社　一平不動産　代表取締役　廣木　正雄
【ハ．郵便番号】　252-0804
【ニ．住所】　藤沢市湘南台1丁目1番地の21

【２．代理者】
【イ．資格】　（　一級　）建築士（　建設大臣　）登録第　264131　号
【ロ．氏名】　築井　准一
【ハ．建築士事務所名】　（　一級　）建築士事務所（　神奈川県　）知事登録第　8066　号
株式会社　一平不動産　一級建築士事務所
【ニ．郵便番号】　252-0804
【ホ．所在地】　藤沢市湘南台1丁目1番地の21
【ヘ．電話番号】　0466-46-4711

【３．設計者】
(代表となる設計者)
【イ．資格】　（　一級　）建築士（　建設大臣　）登録第　264131　号
【ロ．氏名】　築井　准一
【ハ．建築士事務所名】　（　一級　）建築士事務所（　神奈川県　）知事登録第　8066　号
株式会社　一平不動産　一級建築士事務所
【ニ．郵便番号】　252-0804
【ホ．所在地】　藤沢市湘南台1丁目1番地の21
【ヘ．電話番号】　0466-46-4711
【ト．作成又は確認した設計図書】　■設計図書一式　□設計図書一式（構造設計図書を除く）
□設計図書一式（構造計算書を除く）　□

(その他の設計者)
【イ．資格】　（　）建築士（　）登録第　号
【ロ．氏名】
【ハ．建築士事務所名】　（　）建築士事務所（　）知事登録第　号
【ニ．郵便番号】
【ホ．所在地】
【ヘ．電話番号】
【ト．作成又は確認した設計図書】　□構造設計図書一式　□構造計算書一式　□

【イ．資格】　（　）建築士（　）登録第　号
【ロ．氏名】
【ハ．建築士事務所名】　（　）建築士事務所（　）知事登録第　号
【ニ．郵便番号】
【ホ．所在地】
【ヘ．電話番号】
【ト．作成又は確認した設計図書】　□構造図一式　□

この用紙には、複数の不正防止処理を施してあります。

【イ．資格】　（　　）建築士（　　）登録第　　号
【ロ．氏名】
【ハ．建築士事務所名】　（　　）建築士事務所（　　）知事登録第　　号

【ニ．郵便番号】
【ホ．所在地】
【ヘ．電話番号】
【ト．作成又は確認した設計図書】

（構造設計一級建築士又は設備設計一級建築士である旨の表示をした者）
上記設計者のうち、
□建築士法第２０条の２第１項の表示をした者
【イ．氏名】
【ロ．資格】　構造設計一級建築士交付第　　号

□建築士法第２０条の２第３項の表示をした者
【イ．氏名】
【ロ．資格】　構造設計一級建築士交付第　　号

□建築士法第２０条の３第１項の表示をした者
【イ．氏名】
【ロ．資格】　設備設計一級建築士交付第　　号
【イ．氏名】
【ロ．資格】　設備設計一級建築士交付第　　号
【イ．氏名】
【ロ．資格】　設備設計一級建築士交付第　　号

□建築士法第２０条の３第３項の表示をした者
【イ．氏名】
【ロ．資格】　設備設計一級建築士交付第　　号
【イ．氏名】
【ロ．資格】　設備設計一級建築士交付第　　号
【イ．氏名】
【ロ．資格】　設備設計一級建築士交付第　　号

【４．建築設備の設計に関し意見を聴いた者】
（代表となる建築設備の設計に関し意見を聴いた者）
【イ．氏名】
【ロ．勤務先】
【ハ．郵便番号】
【ニ．所在地】
【ホ．電話番号】
【ヘ．登録番号】
【ト．意見を聴いた設計図書】

（その他の建築設備の設計に関し意見を聴いた者）
【イ．氏名】
【ロ．勤務先】
【ハ．郵便番号】
【ニ．所在地】
【ホ．電話番号】
【ヘ．登録番号】
【ト．意見を聴いた設計図書】

この用紙には、複数の不正防止処理を施してあります。
この用紙には、複数の不正防止処理を施してあります。

【イ．氏名】
【ロ．勤務先】
【ハ．郵便番号】
【ニ．所在地】
【ホ．電話番号】
【ヘ．登録番号】
【ト．意見を聴いた設計図書】

【イ．氏名】
【ロ．勤務先】
【ハ．郵便番号】
【ニ．所在地】
【ホ．電話番号】
【ヘ．登録番号】
【ト．意見を聴いた設計図書】

【５．工事監理者】
（代表となる工事監理者）
【イ．資格】　（　一級　）建築士（　建設大臣　）登録第　264131　号
【ロ．氏名】　築井　准一
【ハ．建築士事務所名】（　一級　）建築士事務所（　神奈川県　）知事登録第　8066　号
株式会社　一平不動産　一級建築士事務所
【ニ．郵便番号】　252-0804
【ホ．所在地】　藤沢市湘南台1丁目1番地の21
【ヘ．電話番号】　0466-46-4711
【ト．工事と照合する設計図書】　■設計図書一式　□

（その他の工事監理者）
【イ．資格】　（　）建築士（　）登録第　号
【ロ．氏名】
【ハ．建築士事務所名】（　）建築士事務所（　）知事登録第　号

【ニ．郵便番号】
【ホ．所在地】
【ヘ．電話番号】
【ト．工事と照合する設計図書】

【イ．資格】　（　）建築士（　）登録第　号
【ロ．氏名】
【ハ．建築士事務所名】（　）建築士事務所（　）知事登録第　号

【ニ．郵便番号】
【ホ．所在地】
【ヘ．電話番号】
【ト．工事と照合する設計図書】

【イ．資格】　（　）建築士（　）登録第　号
【ロ．氏名】
【ハ．建築士事務所名】（　）建築士事務所（　）知事登録第　号

【ニ．郵便番号】
【ホ．所在地】
【ヘ．電話番号】
【ト．工事と照合する設計図書】

この用紙には、複数の不正防止処理を施してあります。

【6．工事施工者】

【イ．氏名】　株式会社　一平不動産　代表取締役　廣木　正雄

【ロ．営業所名】　建設業の許可（　神奈川県知事　）第　(特-28) 48908　号

株式会社　一平不動産

【ハ．郵便番号】　252-0804

【ニ．所在地】　藤沢市湘南台1丁目1番地の21

【ホ．電話番号】　0466-46-0088

【7．備考】

【名称のﾌﾘｶﾞﾅ】　ﾑﾂｱｲ55ｷ10ｸｶｸ

【名称】　六会55期10区画

この用紙には、複数の不正防止処理を施してあります。

この用紙には、複数の不正防止処理を施してあります。

管理番号　：H29確申建築藤沢市001775　交付　：2026年（令和8年）　9月　3日

1775

建築計画概要書（第二面）

建築物及びその敷地に関する事項

【１．地名地番】　藤沢市西俣野字北窪306-12

【２．住居表示】

【３．都市計画区域及び準都市計画区域の内外の別等】

■都市計画区域内　（■市街化区域　□市街化調整区域　□区域区分非設定）

□準都市計画区域内　□都市計画区域及び準都市計画区域外

【４．防火地域】　□防火地域　□準防火地域　■指定なし

【５．その他の区域、地域、地区又は街区】■法第２２条指定区域　□高度地区（第　種）

□法第５３条の２最低敷地面積規制区域（　㎡）□法第５４条外壁後退規制区域（　m）□宅造規制区域

■下水道処理区域内　□風致地区（第　種）　□緑化地域　□不燃化推進地域　□土砂災害特別警戒区域

□

【６．道路】敷地が２m以上接している道路のうち幅員が最大なものについて記載

【イ．幅員】　6.000 m

【ロ．敷地と接している部分の長さ】　9.470 m

【７．敷地面積】

【イ．敷地面積】（1）（121.47 ㎡）（　㎡）（　㎡）

（2）（　㎡）（　㎡）（　㎡）

【ロ．用途地域等】（第１種低層）（　）（　）

【ハ．建築基準法第５２条第１項及び第２項の規定による建築物の容積率】

（80.00 %）（　%）（　%）

【ニ．建築基準法第５３条第１項の規定による建築物の建蔽率】　）（

（40.00 %）（　%）（　%）

【ホ．敷地面積の合計】（1）121.47 ㎡

（2）　㎡

【ヘ．敷地に建築可能な延べ面積を敷地面積で除した数値】　%

【ト．敷地に建築可能な建築面積を敷地面積で除した数値】　50.00 %

【チ．備考】　□ 加重平均　■ 角地緩和　□ 風致地区　□

【８．主要用途】　■（区分08010）一戸建ての住宅　□（区分08020）長屋　□（区分08030）共同住宅

【９．工事種別】

■ 新築　□ 増築　□ 改築　□ 大規模の模様替え　□ 大規模の修繕　□ 用途変更　□ 移転

	（申請部分）	（申請以外の部分）	（合計）
【１０．建築面積】			
【イ．建築面積】	（53.82 ㎡）	（　㎡）	（53.82 ㎡）
【ロ．建蔽率】			44.31 %
【１１．延べ面積】			
【イ．建築物全体】	（95.23 ㎡）	（　㎡）	（95.23 ㎡）
【ロ．地階の住宅または老人ホーム、福祉ホームその他これらに類するものの部分】	（　㎡）	（　㎡）	（　㎡）
【ハ．エレベーターの昇降路の部分】	（　㎡）	（　㎡）	（　㎡）
【ニ．共同住宅の共用の廊下等の部分】	（　㎡）	（　㎡）	（　㎡）
【ホ．自動車車庫等の部分】	（　㎡）	（　㎡）	（　㎡）
【ヘ．備蓄倉庫の部分】	（　㎡）	（　㎡）	（　㎡）
【ト．蓄電池の設置部分】	（　㎡）	（　㎡）	（　㎡）
【チ．自家発電設備の設置部分】	（　㎡）	（　㎡）	（　㎡）
【リ．貯水槽の設置部分】	（　㎡）	（　㎡）	（　㎡）
【ヌ．住宅の部分】	（95.23 ㎡）	（　㎡）	（95.23 ㎡）
【ル．老人ホーム、福祉ホームその他これらに類するものの部分】	（　㎡）	（　㎡）	（　㎡）
【ヲ．延べ面積】			95.23 ㎡
【ワ．容積率】			78.40 %

整理番号 20260903 窓口02 0003 06　5/8

この用紙には、複数の不正防止処理を施してあります。

この用紙には、複数の不正防止処理を施してあります。

【１２．建築物の数】
【イ．申請に係る建築物の数】　■１棟　□２棟　□３棟　□　棟
【ロ．同一敷地内の他の建築物の数】　■なし　□１棟　□２棟　□　棟

【１３．建築物の高さ等】　（申請に係る建築物）（他の建築物）
【イ．最高の高さ】　（8.130 m）（　m）
【ロ．階数】　地上　（2 階）（　階）
地下　（0 階）（　階）
【ハ．構造】
■木造（■軸組工法　□枠組壁工法）　□
□ＲＣ造　□Ｓ造　□ＳＲＣ造　一部　造
【ニ．建築基準法第５６条第７項の規定による特例の適用の有無】　□ 有　■ 無
【ホ．適用があるときは、特例の区分】
□ 道路高さ制限不適用　□ 隣地高さ制限不適用　□ 北側高さ制限不適用

【１４．許可・認定等】

■ 開発行為許可：	第	指令開業第29号-124	号	（平成 29 年 8 月 17 日）
検査済：	第	開業316	号	（平成 30 年 1 月 11 日）
完了公告：	第	275	号	（平成 30 年 1 月 12 日）
□ 宅地造成に関する工事許可：	第		号	（平成　年　月　日）
検査済：	第		号	（平成　年　月　日）
□ 位置指定道路：	第		号	（平成　年　月　日）
□ 急傾斜地崩壊危険区域の許可：	第		号	（平成　年　月　日）
□ 法第４３条ただし書き許可：	第		号	（平成　年　月　日）
□ 狭あい道路協議済：	第		号	（平成　年　月　日）
■ 開発行為変更許可	第	指令開業第29号-237	号	（平成 29 年 11 月 24 日）
□	第		号	（平成　年　月　日）

【１５．工事着手予定年月日】　平成　30 年 2 月 16 日

【１６．工事完了予定年月日】　平成　30 年 5 月 17 日

【１７．特定工程工事終了予定年月日】　（特定工程）

（第 1 回）	平成	30	年	3	月	8	日（屋根の小屋組及び構造耐力上主要な軸組の工事）
（第　回）	平成		年		月		日（　）
（第　回）	平成		年		月		日（　）

【１８．その他必要な事項】
□ 法第５３条の２第３項適用
■ 住宅用火災警報器
□


【１９．備考】

この用紙には、複数の不正防止処理を施してあります。


建築計画概要書（第三面）

付近見取図

申請地：藤沢市西俣野字北窪306-12

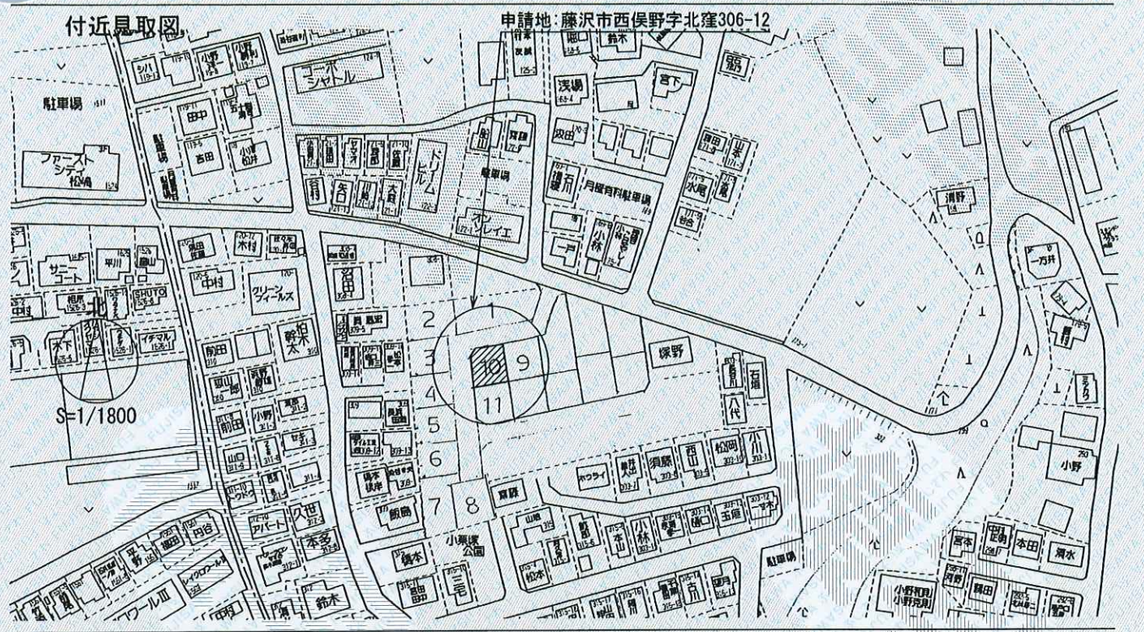

配置図

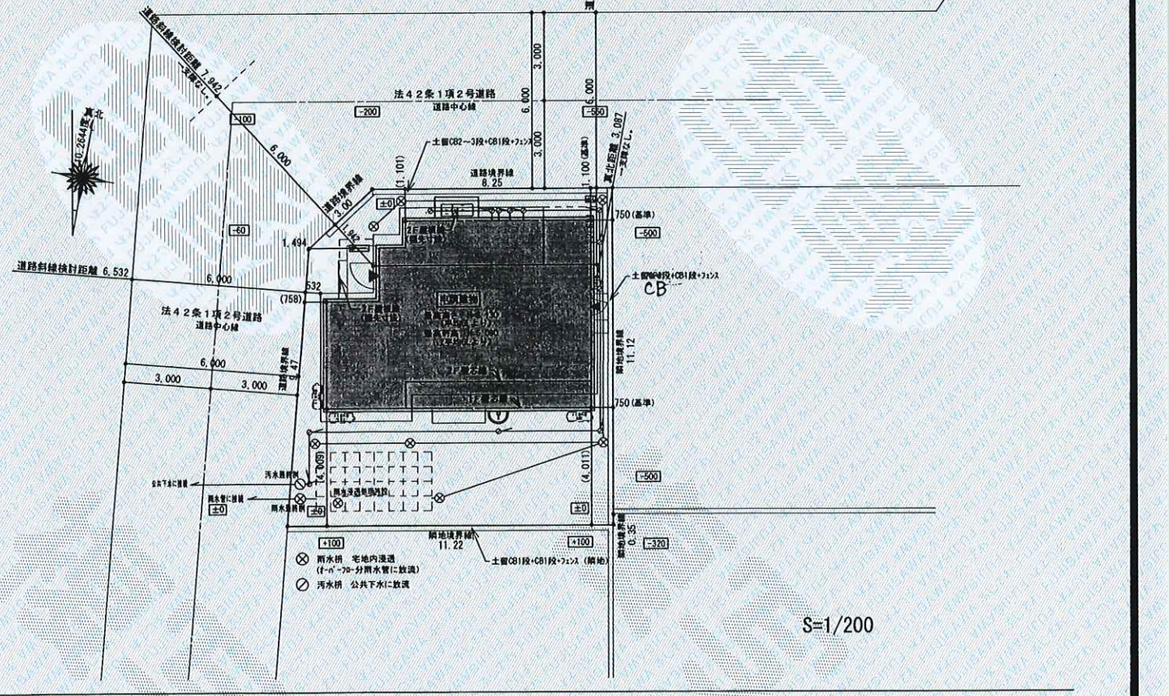

この用紙には、複数の不正防止処理を施してあります。

管理番号　：H29確申建築藤沢市001775　交付　：2026年（令和8年）　9月　3日

この用紙には、複数の不正防止処理を施してあります。

これは、藤沢市で保管する建築計画概要書の写しであることを証明します。


2026年（令和8年）9月 3日

藤　沢　市　長　　鈴 木 恒 夫

整理番号 20260903-窓口02-0003-06　　8/8

この用紙には、複数の不正防止処理を施してあります。

藤沢市指定道路図

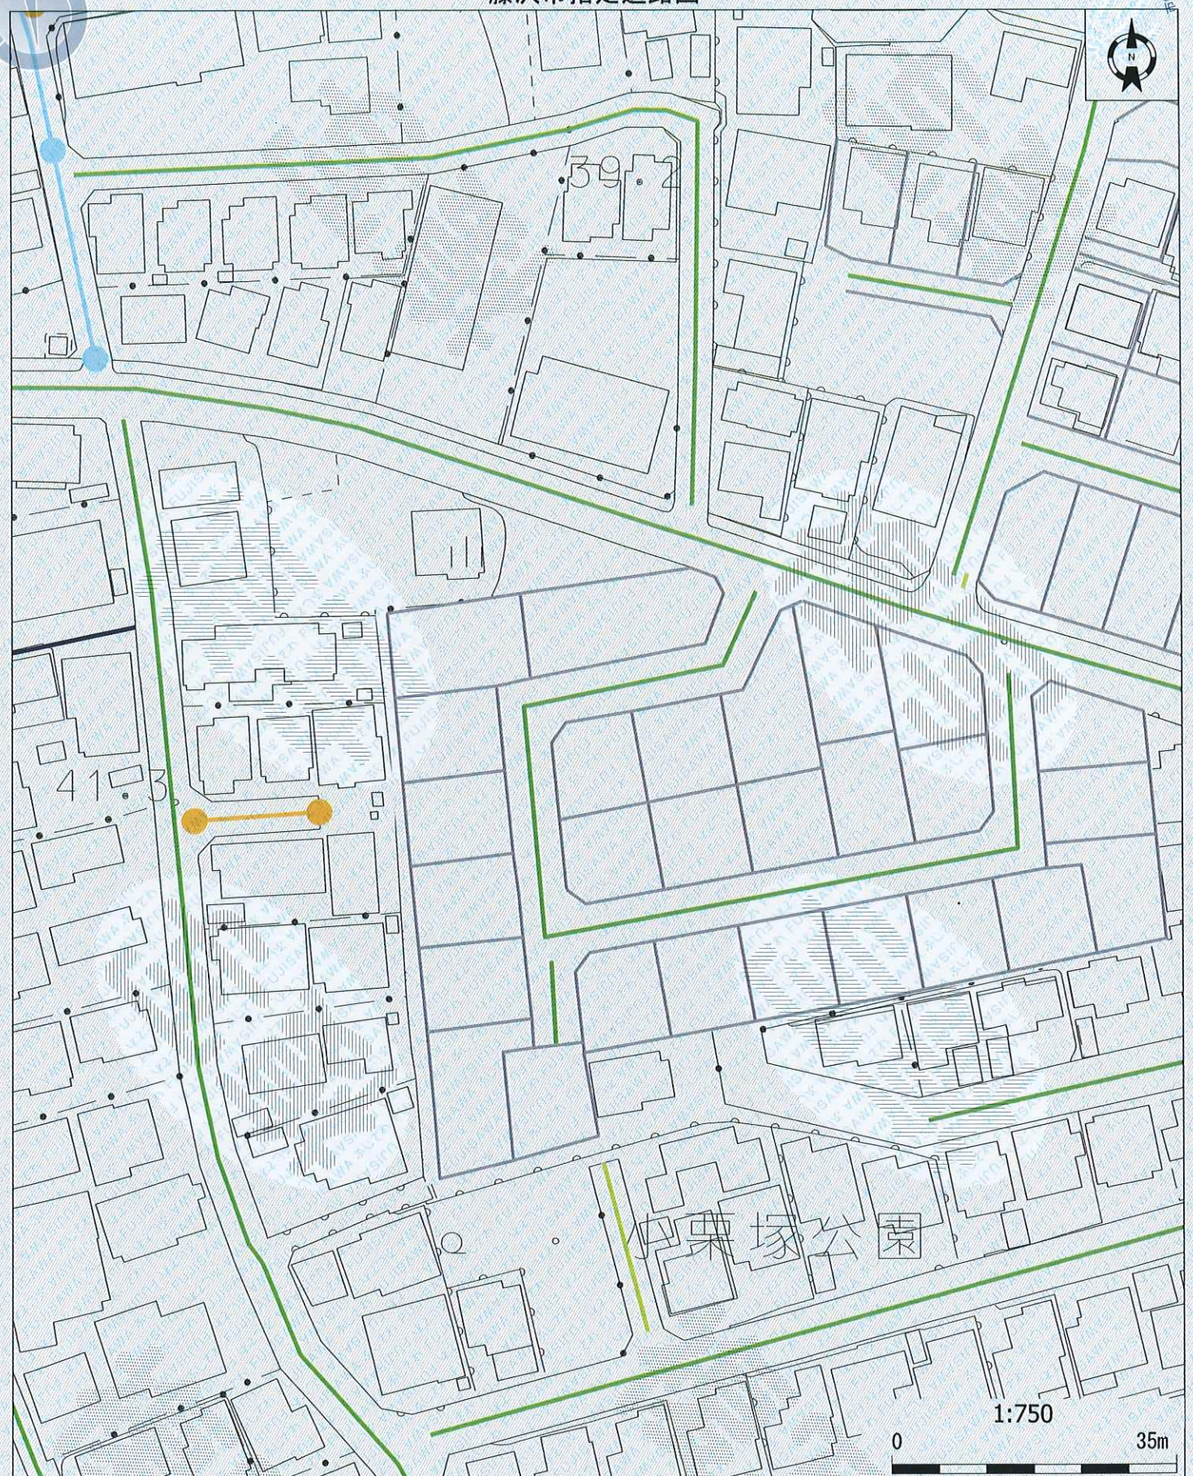

凡例	1号道路	1号道路（調査中）	復元必要な1号道路	2号道路	3号道路	3号道路（確定済）	4号道路	5号道路	2項道路	2項道路（未確定）	3項道路	3項道路（未確定）	法外の道	特定道路	特定道路（確定済）

（指定道路図の注意事項）
・建築基準法上の道路種別のみを示したものであり、表示している内容すべてを証明するものではありません。
・表示に利用している地図は土地の境界や権利関係を示すものではありません。
・道路の位置および種別は、変更する場合があります。建築確認等の際は、必ず最新の情報を確認してください。
・本図は建築基準法に規定される道路と概ねの位置を参考として表示しています。接道状況等については、必ず現地を確認してください。
・行政界に位置する道路または横断する道路については、当該道路を所管する行政庁にも確認してください。
・道路種別を示す線データについては、地図の精度及びデータ作成上の誤差(ずれ)が生じている場合があります。
・本図の著作権は藤沢市に帰属します。いかなる形式においても著作権者に無断で本図の全部または一部を複製し、利用することを禁じます。
・藤沢市は本図の利用により発生した直接、または間接の損失、損害等について一切の責任を負いません。

この指定道路図は、藤沢市が作成し、保管しているものの写しに相違ありません。

2026年（令和8年）9月3日

藤沢市長　鈴　木　恒　夫

20260903-窓口02-0003-07

この用紙には、複数の不正防止処理を施してあります。

管理番号：H29-023

これは、開発登録簿の写であることを証する。
2026年（令和8年） 9月 3日

藤沢市長　　鈴　木　恒　夫

N

308-1
（木造二階建）

309-5
（木造二階建）

309-6

309-16
（木造二階建）

309-17
（木造二階建）

309-13
（木造二階建）

309-1
（木造二階建）

313-2
（木造二階建）

315-8
（木造二階建）

315-9
小糸塚公園

304-1

304-6
（木造二階建）

304-4
（木造二階建）

303-7
（木造二階建）

303-8
（木造二階建）

303-9
（木造二階建）

303-10
（木造二階建）

303-18
（木造二階建）

303-4
（木造二階建）

307-3
（木造二階建）

1 専用住宅 243.07㎡ FL=13.20
2 専用住宅 188.53㎡ FL=13.80
3 専用住宅 135.09㎡ FL=13.80
4 専用住宅 135.06㎡ FL=13.80
5 専用住宅 135.08㎡ FL=13.80
6 専用住宅 135.09㎡ FL=13.80
7 専用住宅 179.20㎡ FL=13.80
8 専用住宅 135.00㎡ FL=13.50
9 専用住宅 125.52㎡ FL=12.40
10 専用住宅 121.47㎡ FL=12.90
11 専用住宅 123.20㎡ FL=13.00

造成協力地1 23.50㎡
造成協力地2 29.01㎡
開発道路 480.94㎡

T4 (12.151)
T3 △(10.010)
T8-1 (14.681)

市道（下屋敷小糸塚線）
市道（大全196号線）
市道（大全198号線）

幅員=7.31
幅員=6.00
幅員=16.00

既設給水管（φ100）
既設汚水本管 φ900
既設雨水本管 φ250
L型側溝
歩道 AS
開知擁壁
待ち受け擁壁
RC擁壁(L-1.0)
RC擁壁(L-1.5)
CB積(1～3段)
CB積(1～2段)
CB積(2段)
CB積(1段)
自然法面
既設擁壁撤去工事による擁壁
既設擁壁撤去工事による擁壁（クレーチング）
既設擁壁撤去工事による擁壁（一部切り）
駐車スペース
物置
カーブミラー
仕切弁
消火栓
汚水
雨水
天端
AS
CO
EP

No.0 11.52
No.1 12.18
No.2 12.84
No.3 13.08
No.0+11.09 11.80
No.1+16.85 12.81
No.1+12.23 12.73
No.3+18.93 13.30

L=8.91 4.4%
L=12.23 4.4%
L=4.62 1.7%
L=23.15 0.9%
L=20.00 1.2%
L=18.93 1.1%
L=11.09 2.5%

※既設擁壁は、経年劣化によるクラック等は見られず構造上安全である。


凡　例	
申請区域	
既設CB積	
既設間知擁壁	
既設自然法面	
既存建築物	
既設汚水人孔	汚水
既設雨水人孔	雨水
現況レベル	10.00
測量多角点	△ T1
新設RC擁壁	
待ち受け擁壁	
新設CB積	
新設法面施工(30)	

凡　例	
新設L型側溝・雨水桝	
新設汚水人孔・汚水本管	
新設雨水人孔・雨水本管	
新設汚水取付桝・取付管	
新設雨水取付桝・取付管	
新設給水管	
雨水浸透溝・宅内最終桝(塩ビ桝)	
転落防止防護柵	
区画番号 建物用途 敷地面積 計画地盤高	0 専用住宅 150.00㎡ FL=20.00

図面名	土地利用計画図（竣工図）	縮尺	1/300
所在地	藤沢市西俣野字北窪306-1ほか		
図面作製	株式会社 H02開発設計事務所 小林道雄		

整理番号 20260903-窓口02-0003-03

藤沢市公共下水道台帳図

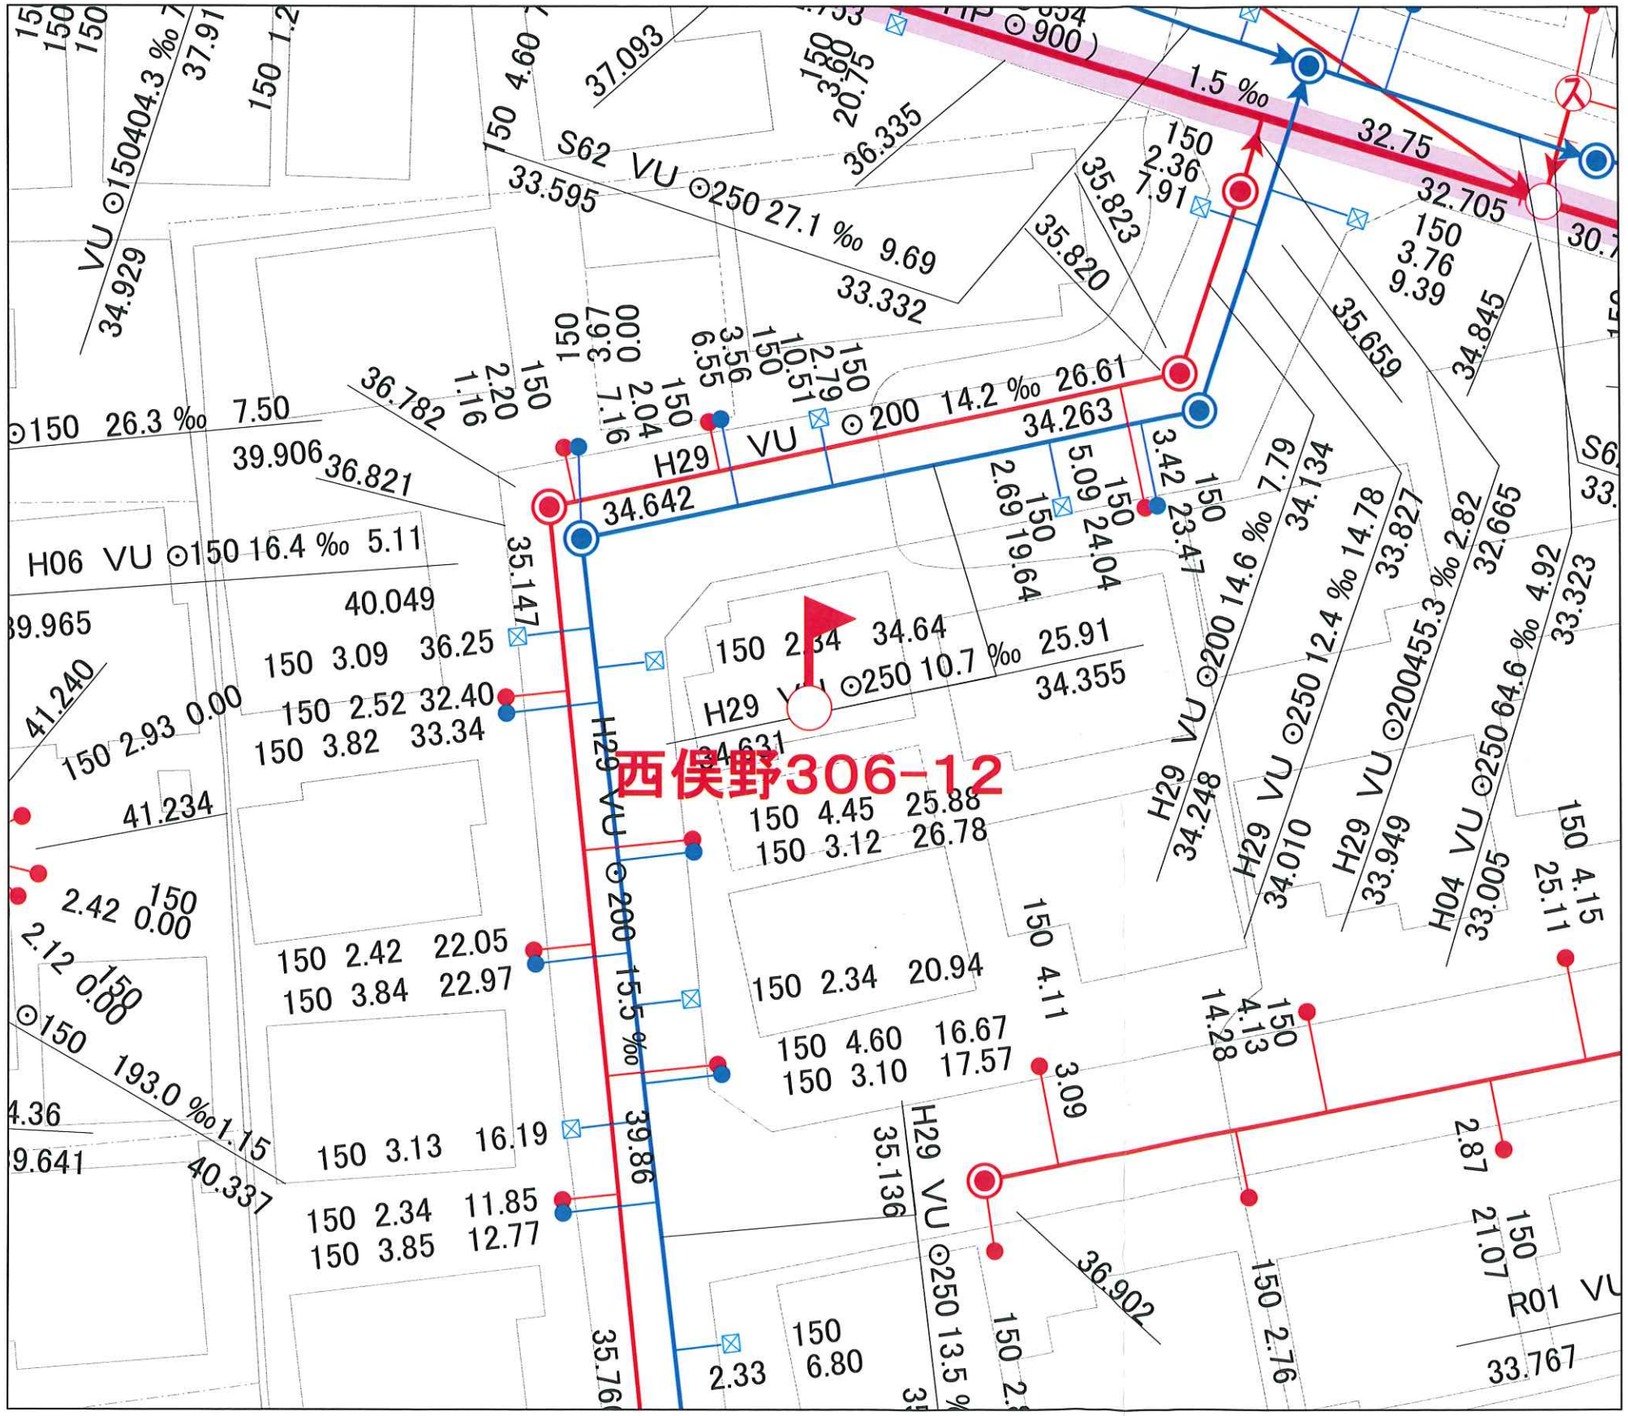

1:250

藤沢市道路下水道部下水道管路課では、できる限り最新で正確な情報の提供に努めておりますが、下水道の工事や道路工事等が行われた場合、しばらくの間、図面と現地が整合しないことがあります。したがって、本図面を設計、工事等にご利用される場合は、**下水道施設の位置などを現地で調査・確認のうえ、ご利用ください。**

【凡例】

ます


- 宅地汚水桝
- 宅地雨水桝
- 宅地合流桝
- 集水雨水桝

マンホール

- 0号マンホール（内径75cm円形）
- 特0号マンホール（内径75cm円形）
- 1号マンホール（内径90cm円形）
- 特1号マンホール（内径90cm円形）
- 2号マンホール（内径120cm円形）
- 特2号マンホール（内径120cm円形）
- 3号マンホール（内径150cm円形）
- 特3号マンホール（内径150cm円形）
- 4号マンホール（内径180cm円形）
- 特4号マンホール（内径180cm円形）
- 5号マンホール（内法210×120角型）
- 特5号マンホール（内法210×120角型）

管渠

- 幹線
- 幹線圧送管
- 支線
- 支線圧送管

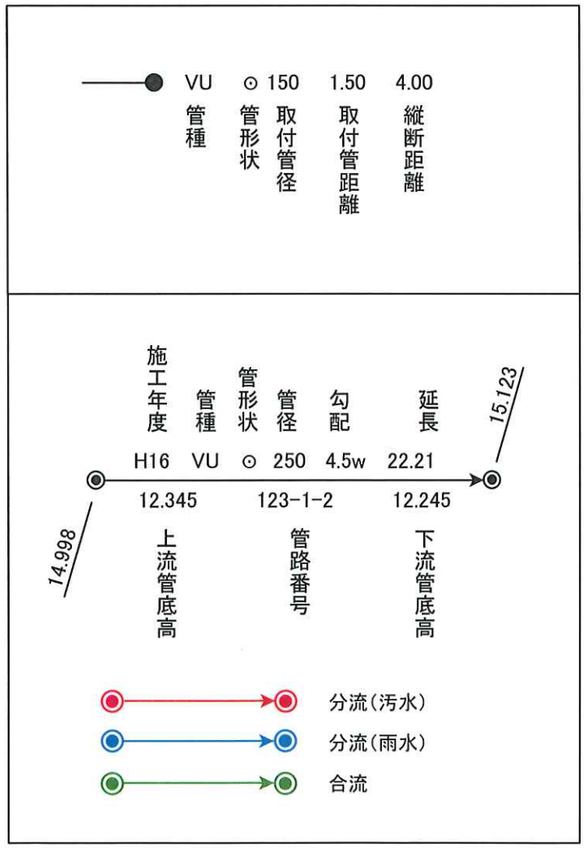

藤沢市