
平　面　図　S=1:250

城山四丁目

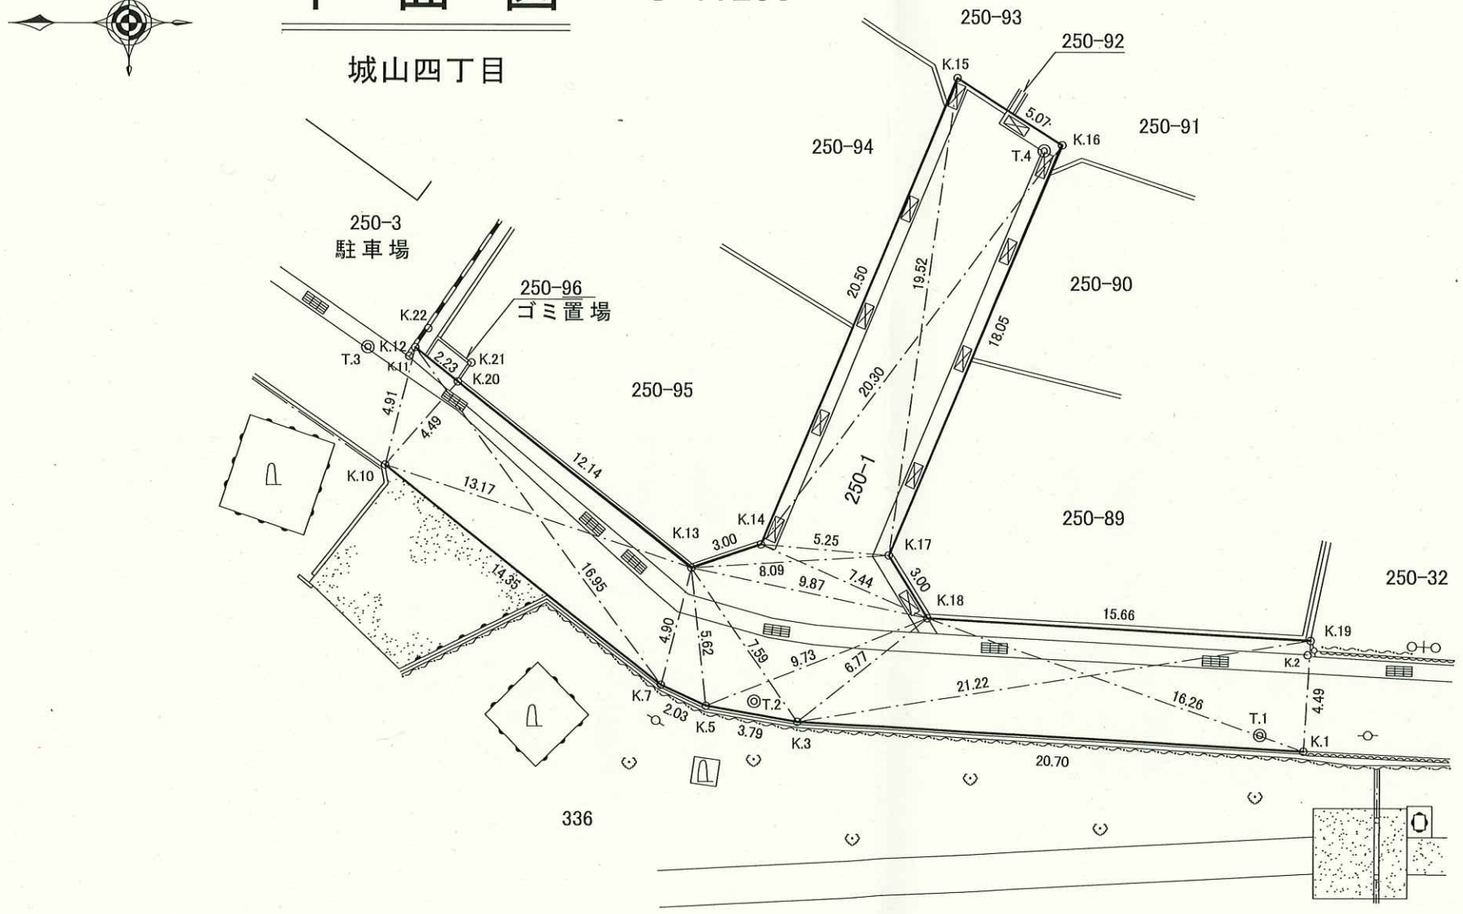

小田原市
土木管理課
令和 7.4.21
境界確定図写
発　行