表示年月日：２０２５／０４／２１

イ　318-4

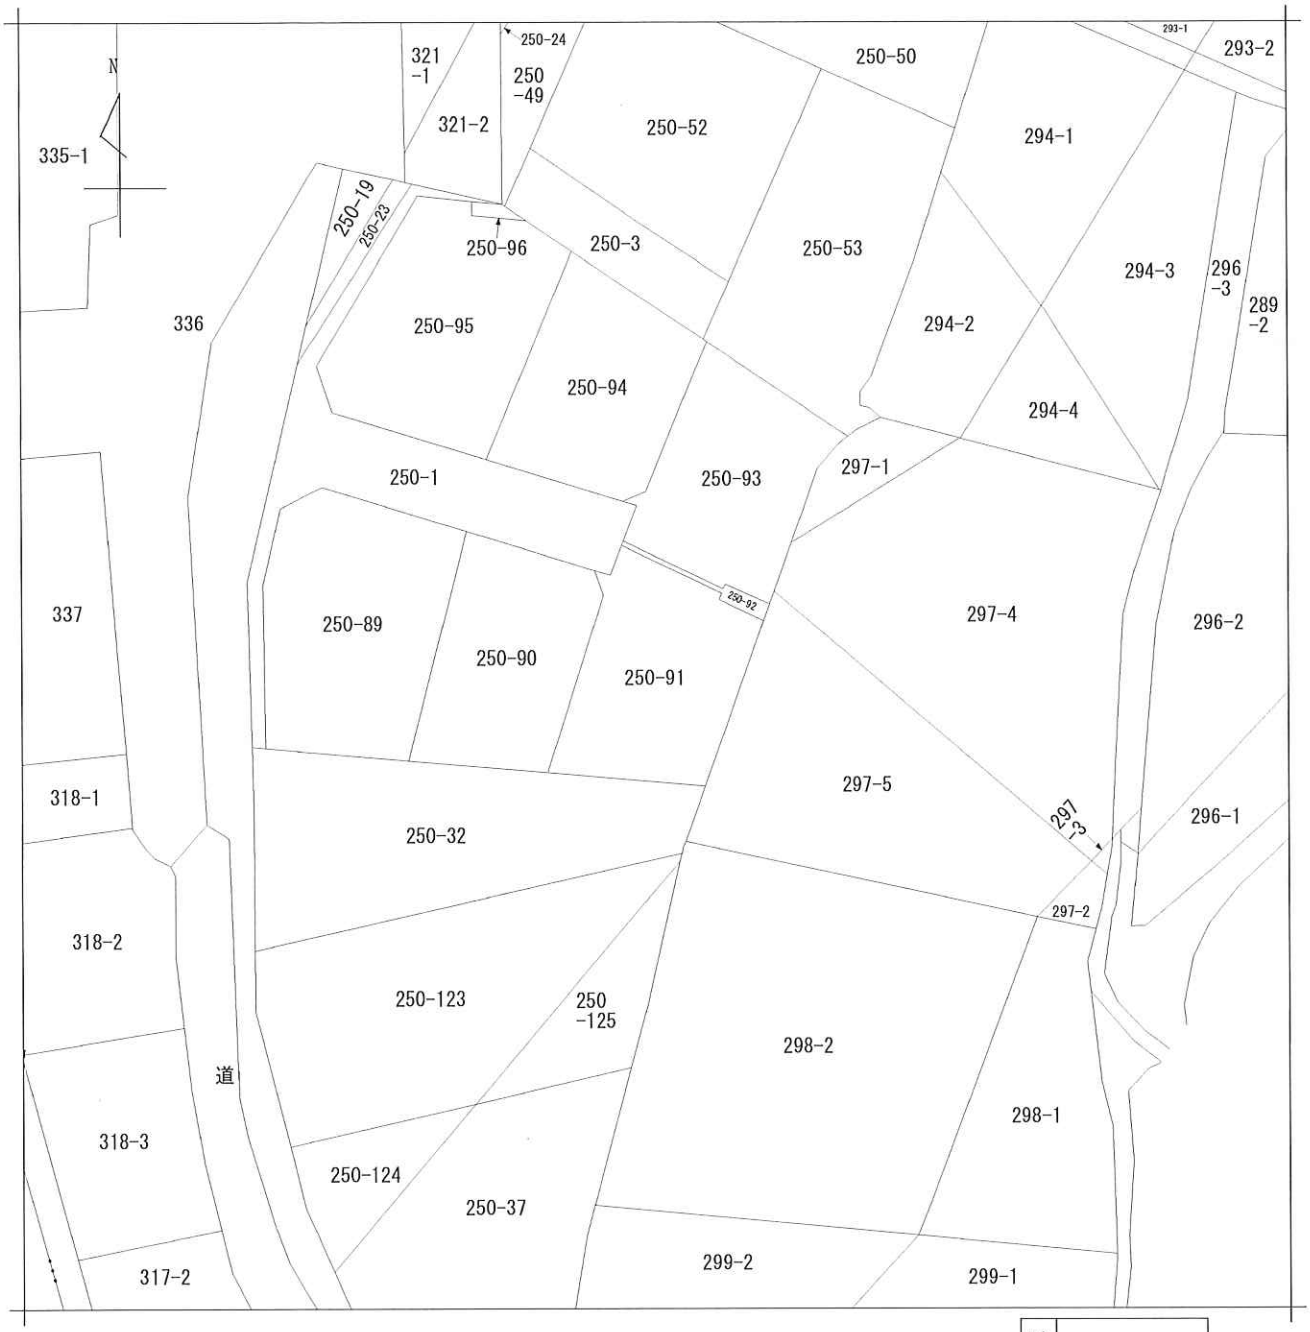
N
250-24
293-1
293-2
321
-1
250
-49
250-50
250-52
321-2
294-1
335-1
250-19
250-23
250-96
250-3
250-53
294-3
296
-3
289
-2
336
250-95
294-2
250-94
294-4
250-1
297-1
250-93
250-92
337
250-89
297-4
296-2
250-90
250-91
318-1
297-5
297
-3
296-1
250-32
297-2
318-2
250-123
250
-125
298-2
道
298-1
318-3
250-124
250-37
299-2
299-1
317-2

地番区域見出	城山４丁目

請求部分	所在	小田原市城山四丁目				地番	250番91		
出力縮尺	1/300	精度区分		座標系番号又は記号		分類	地図に準ずる図面	種類	旧土地台帳附属地図
作成年月日				備付年月日(原図)			補記事項		

２０２５／１１／１４　１１：２８　現在の情報です。

表題部　（主である建物の表示）	調製　平成１６年８月２６日	不動産番号	０２０３０００４００４４６
所在図番号	余白		
所在	小田原市城山四丁目　２５０番地９１		余白
家屋番号	２５０番９１		余白
①　種類	②　構造	③　床面積　㎡	原因及びその日付〔登記の日付〕
居宅	木造スレート葺２階建	１階　４７：５１ ２階　４２：９６	平成１５年９月８日新築 〔平成１５年９月１６日〕
余白	余白	余白	昭和６３年法務省令第３７号附則第２条第２項の規定により移記 平成１６年８月２６日

権利部（甲区）（所有権に関する事項）			
順位番号	登記の目的	受付年月日・受付番号	権利者その他の事項
１	所有権保存	平成１５年９月２４日 第２０１８４号	所有者　小田原市城山四丁目２０番１８号 土　井　正　好 順位１番の登記を移記
付記１号	１番登記名義人住所変更	令和７年７月１４日 第３２３０５号	原因　令和７年１月１７日住所移転 住所　兵庫県西宮市枝川町５番１５－１２０１号
	余白	余白	昭和６３年法務省令第３７号附則第２条第２項の規定により移記 平成１６年８月２６日
２	所有権移転	令和７年７月１４日 第３２３０７号	原因　令和７年７月１４日売買 所有者　平塚市見附町２９番１３号 株式会社シティクリエイション 会社法人等番号　０２１０－０１－０６２８７４

権利部（乙区）（所有権以外の権利に関する事項）			
順位番号	登記の目的	受付年月日・受付番号	権利者その他の事項
１	抵当権設定	平成１５年９月２４日 第２０１８５号	原因　平成１５年３月１１日保証委託契約による求償債権平成１５年９月２４日設定 債権額　金３，６００万円 損害金　年１４％（年３６５日日割計算） 債務者　小田原市城山四丁目２０番１８号 土　井　正　好 抵当権者　横浜市西区みなとみらい三丁目１番１号 横浜信用保証株式会社 共同担保　目録㋚第１９５０号 順位１番の登記を移記
	余白	余白	昭和６３年法務省令第３７号附則第２条第２項の規定により移記 平成１６年８月２６日
２	１番抵当権抹消	令和７年７月１４日 第３２３０６号	原因　令和７年７月１４日主債務消滅
３	根抵当権設定	令和７年７月１４日 第３２３０８号	原因　令和７年７月１４日設定 極度額　金２，６００万円 債権の範囲　信用金庫取引　手形債権　小切手債権　電子記録債権 債務者　平塚市見附町２９番１３号 株式会社シティクリエイション 根抵当権者　平塚市紅谷町１１番１９号 平塚信用金庫 共同担保　目録㋥第６２２２号

共同担保目録			
記号及び番号	㋚第１９５０号	調製	平成１７年５月２６日
番号	担保の目的である権利の表示	順位番号	予備
１	小田原市城山四丁目　２５０番９１の土地	１	令和７年７月１４日受付第３２３０６号抹消

2	小田原市城山四丁目　２５０番地９１　家屋番号　２５０番９１の建物	1	令和７年７月１４日受付第３２３０６号抹消
	余 白	余 白	平成１７年法務省令第１８号附則第１４条の規定により移記 平成１７年５月２６日
	余 白	余 白	令和７年７月１４日全部抹消

共　同　担　保　目　録			
記号及び番号	(に)第６２２２号	調製	令和７年７月１４日
番　号	担保の目的である権利の表示	順位番号	予　備
1	小田原市城山四丁目　２５０番９１の土地	3	余 白
2	小田原市城山四丁目　２５０番地９１　家屋番号　２５０番９１の建物	3	余 白

＊　「登記の目的」欄に「相続人申告」と記載されている登記は、所有権の登記名義人（所有者）の相続人からの申出に基づき、登記官が職権で、申出があった相続人の住所・氏名等を付記したものであり、権利関係を公示するものではない。
＊　下線のあるものは抹消事項であることを示す。

登記年月日： 平成15年9月16日

表示年月日：2025/04/21

051671　各階平面図

家屋番号	250番91
建物の所在	小田原市城山四丁目２５０番地９１

建物図面
~~各階平面図~~

1階

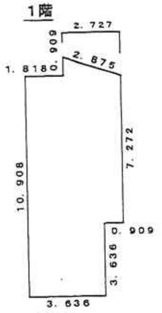

2.727
0.909
2.875
1.8180
10.908
7.272
0.909
3.636
3.636

求積表

0.909 × 2.727 / 2= 1.2394
4.545 × 7.272 = 33.0512
3.636 × 3.636 = 13.2205
計 47.5111

床面積 47.51 ㎡

2階

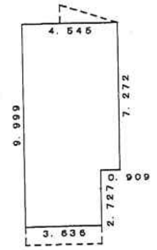

4.545
9.999
7.272
0.909
2.7270
3.636

求積表

4.545 × 7.272 = 33.0512
3.636 × 2.727 = 9.9154
計 42.9666

床面積 42.96 ㎡

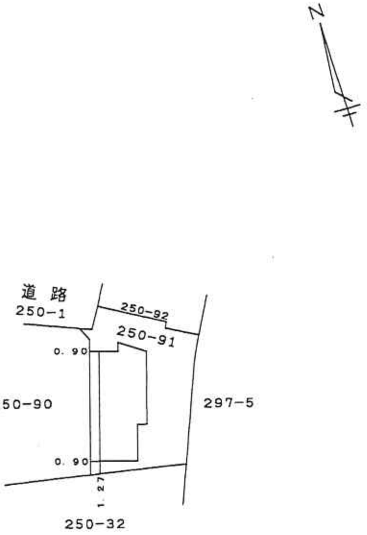

N
道路
250-1
250-92
250-91
0.90
250-90
297-5
0.90
1.27
250-32

（日調連12）

（日加納）

作製者	小田原市柳新田42番地5 土地家屋調査士　渡部泰夫 登録　第708号　（平成15年　9月10日作製）	縮尺	1/250
申請人	土　井　正　好	縮尺	1/500

15.9.16

（日本土地家屋調査士会連合会用紙）

２０２５／１１／１４　１１：２７　現在の情報です。

表題部　（土地の表示）	調製	平成１６年８月２６日	不動産番号	０２０３０００２６９５３１
地図番号	余白	筆界特定	余白	
所在	小田原市城山四丁目		余白	

①地番	②地目	③地積　㎡	原因及びその日付〔登記の日付〕
２５０番９１	宅地	１４７：０７	２５０番１から分筆 〔平成１４年１０月２１日〕
余白	余白	余白	昭和６３年法務省令第３７号附則第２条第２項の規定により移記 平成１６年８月２６日

権利部（甲区）（所有権に関する事項）

順位番号	登記の目的	受付年月日・受付番号	権利者その他の事項
１	所有権移転	平成１５年３月１１日 第４７７８号	原因　平成１５年３月１１日売買 所有者　小田原市東町一丁目２０番１８－４０７号コンセール小田原東町 土井正好 順位２番の登記を移記
付記１号	１番登記名義人表示変更	平成１５年９月２５日 第２０３６１号	原因　平成１５年９月９日住所移転 住所　小田原市城山四丁目２０番１８号 順位２番付記１号の登記を移記
付記２号	１番登記名義人住所変更	令和７年７月１４日 第３２３０５号	原因　令和７年１月１７日住所移転 住所　兵庫県西宮市枝川町５番１５－１２０１号
	余白	余白	昭和６３年法務省令第３７号附則第２条第２項の規定により移記 平成１６年８月２６日
２	所有権移転	令和７年７月１４日 第３２３０７号	原因　令和７年７月１４日売買 所有者　平塚市見附町２９番１３号 株式会社シティクリエイション 会社法人等番号　０２１０－０１－０６２８７４

権利部（乙区）（所有権以外の権利に関する事項）

順位番号	登記の目的	受付年月日・受付番号	権利者その他の事項
１	抵当権設定	平成１５年３月１１日 第４７７９号	原因　平成１５年３月１１日保証委託契約による求償債権同日設定 債権額　金３，６００万円 損害金　年１４％（年３６５日日割計算） 債務者　小田原市東町一丁目２０番１８－４０７号コンセール小田原東町 土井正好 抵当権者　横浜市西区みなとみらい三丁目１番１号 横浜信用保証株式会社 順位３番の登記を移記
付記１号	１番抵当権担保追加	余白	共同担保　目録（さ）第１９５０号 平成１５年９月２４日付記 順位３番付記１号の登記を移記
	余白	余白	昭和６３年法務省令第３７号附則第２条第２項の規定により移記 平成１６年８月２６日
２	１番抵当権抹消	令和７年７月１４日 第３２３０６号	原因　令和７年７月１４日主債務消滅
３	根抵当権設定	令和７年７月１４日 第３２３０８号	原因　令和７年７月１４日設定 極度額　金２，６００万円 債権の範囲　信用金庫取引　手形債権　小切手債権　電子記録債権 債務者　平塚市見附町２９番１３号 株式会社シティクリエイション 根抵当権者　平塚市紅谷町１１番１９号 平塚信用金庫 共同担保　目録（に）第６２２２号

共　同　担　保　目　録

記号及び番号	(さ)第１９５０号	調製	平成１７年５月２６日
番　号	担保の目的である権利の表示	順位番号	予　　備
1	小田原市城山四丁目　２５０番９１の土地	1	令和７年７月１４日受付第３２３０６号抹消
2	小田原市城山四丁目　２５０番地９１　家屋番号　２５０番９１の建物	1	令和７年７月１４日受付第３２３０６号抹消
	余白	余白	平成１７年法務省令第１８号附則第１４条の規定により移記 平成１７年５月２６日
	余白	余白	令和７年７月１４日全部抹消

共　同　担　保　目　録

記号及び番号	(に)第６２２２号	調製	令和７年７月１４日
番　号	担保の目的である権利の表示	順位番号	予　　備
1	小田原市城山四丁目　２５０番９１の土地	3	余白
2	小田原市城山四丁目　２５０番地９１　家屋番号　２５０番９１の建物	3	余白

＊　「登記の目的」欄に「相続人申告」と記載されている登記は、所有権の登記名義人（所有者）の相続人からの申出に基づき、登記官が職権で、申出があった相続人の住所・氏名等を付記したものであり、権利関係を公示するものではない。

＊　下線のあるものは抹消事項であることを示す。

054556

前 250－1　後・新同一・新

地番	250－89 ～250－96
土地の所在	小田原市城山４丁目

250－1 地積測量図 (1/2)

求積表

地番	Ⓑ 250－89				
NO	境界標	Xn	Yn	Yn+1－Yn-1	Xn・(Yn+1－Yn-1)
Z319	金属鋲	71. 115	107. 894	11. 510	818. 5336
Z318	プレート	86. 563	111. 827	-4. 077	-352. 9173
P16	プレート	89. 985	103. 817	-10. 562	-950. 4215
P15	プレート	88. 408	101. 265	-3. 500	-309. 4280
P3	プレート	72. 770	100. 317	6. 629	482. 3923
				合計	-311. 8409
				合計面積	155. 92045
				地積	155. 92 ㎡

地番	Ⓒ 250－90				
NO	境界標	Xn	Yn	Yn+1－Yn-1	Xn・(Yn+1－Yn-1)
Z320	金属鋲	69. 421	115. 648	11. 990	832. 3577
C88	プレート	82. 050	119. 884	3. 708	304. 2414
Z317	プレート	83. 346	119. 356	-8. 057	-671. 5187
Z318	プレート	86. 563	111. 827	-11. 462	-992. 1851
Z319	プレート	71. 115	107. 894	3. 821	271. 7304
				合計	-255. 3743
				合計面積	127. 68715
				地積	127. 68 ㎡

地番	Ⓓ 250－91				
NO	境界標	Xn	Yn	Yn+1－Yn-1	Xn・(Yn+1－Yn-1)
P1	コンクリート杭	67. 402	124. 890	9. 714	654. 7430
K15	金属鋲	68. 640	125. 362	4. 714	323. 5689
K16	金属鋲	78. 284	129. 604	4. 645	363. 6291
Z327	プレート	79. 024	130. 007	-2. 420	-191. 2380
Z325	プレート	80. 766	127. 184	-2. 541	-205. 2264
C106	プレート	81. 312	127. 466	-5. 502	-447. 3786
Z323	プレート	84. 878	121. 682	-7. 049	-598. 3050
C86	プレート	82. 893	120. 417	-2. 326	-192. 8091
Z317	プレート	83. 346	119. 356	-0. 533	-44. 4234
C88	プレート	82. 050	119. 884	-3. 708	-304. 2414
Z320	金属鋲	69. 421	115. 648	5. 006	347. 5215
				合計	-294. 1594
				合計面積	147. 07970
				地積	147. 07 ㎡

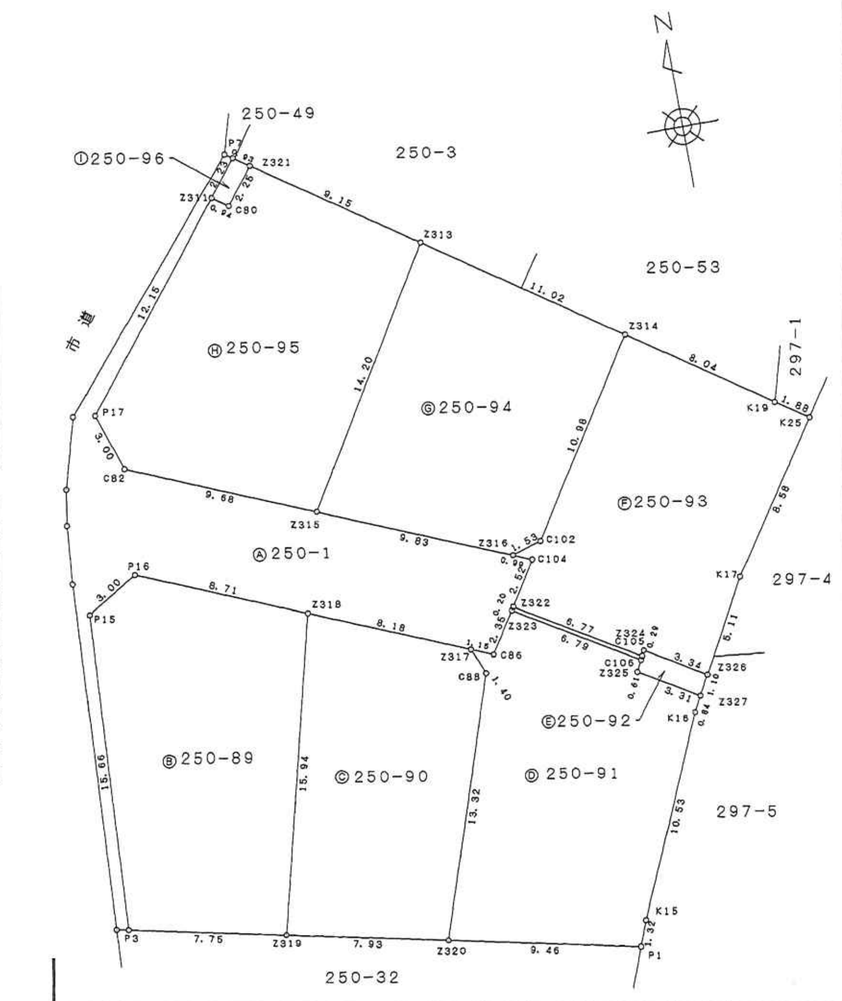
N
250－49
①250－96
P7
93
Z321
2.23
2.25
Z311
0.94
C80
250－3
9.15
Z313
250－53
11.02
Z314
8.04
297－1
K19
1.88
K25
市道
12.15
Ⓗ250－95
14.20
Ⓖ250－94
10.98
P17
3.00
C82
9.68
Z315
9.83
Z316
1.53
C102
0.99
C104
Ⓕ250－93
8.58
Ⓐ250－1
P16
3.00
P15
8.71
Z318
8.18
2.52
0.20
Z322
2.35
Z323
6.77
6.79
Z324
C105
0.29
K17
297－4
6.11
1.15
Z317
C86
C88
1.40
C106
Z325
0.61
3.34
3.31
Z326
1.10
Z327
Ⓔ250－92
K16
0.84
Ⓑ250－89
15.66
15.94
Ⓒ250－90
13.32
Ⓓ250－91
10.53
297－5
K15
1.32
P3
7.75
Z319
7.93
Z320
9.46
P1
250－32

平成壱四年拾月弐壱日　登記

作製者	足柄上郡開成町吉田島[illegible]番地3 土地家屋調査士　石川　徹　(平成14年10月7日作製)	申請人	松浦建設株式会社 代表取締役　松浦秀和
		縮尺	1/250

(神奈川県土地家屋調査士会)

14.10.21

054557

前 250-1 後・新同一・~~新~~

地番	250-89 ~250-96 ← 250-1
土地の所在	小田原市城山4丁目

地積測量図 ②/②

地番	Ⓔ 250-92				
NO	境界標	Xn	Yn	Yn+1-Yn-1	Xn・(Yn+1-Yn-1)
Z327	プレート	79.024	130.007	3.351	264.8094
Z326	プレート	79.994	130.535	-2.316	-185.2661
Z324	プレート	81.748	127.691	-2.977	-243.3637
C105	プレート	81.490	127.558	-5.902	-480.9539
Z322	プレート	85.046	121.789	-5.876	-499.7302
Z323	プレート	84.878	121.682	5.677	481.8524
C106	プレート	81.312	127.466	5.502	447.3786
Z325	プレート	80.766	127.184	2.541	205.2264
				合計	-10.0471
				合計面積	5.02355
				地積	5.02 ㎡

地番	Ⓕ 250-93				
NO	境界標	Xn	Yn	Yn+1-Yn-1	Xn・(Yn+1-Yn-1)
Z326	プレート	79.994	130.535	5.288	423.0082
K17	金属鋲	84.486	132.979	7.245	612.1010
K25	石杭	91.605	137.780	3.244	297.1666
K19	石杭	92.656	136.223	-8.158	-755.8876
Z314	プレート	97.253	129.622	-12.526	-1218.1910
C102	プレート	88.002	123.697	-7.392	-650.5107
Z316	プレート	87.559	122.230	-0.555	-48.5952
C104	プレート	87.170	123.142	-0.441	-38.4419
Z322	プレート	85.046	121.789	4.416	375.5631
C105	プレート	81.490	127.558	5.902	480.9539
Z324	プレート	81.748	127.691	2.977	243.3637
				合計	-279.4699
				合計面積	139.73495
				地積	139.73 ㎡

地番	Ⓖ 250-94				
NO	境界標	Xn	Yn	Yn+1-Yn-1	Xn・(Yn+1-Yn-1)
C102	プレート	88.002	123.697	7.392	650.5107
Z314	プレート	97.253	129.622	-3.118	-303.2348
Z313	プレート	103.550	120.579	-16.438	-1702.1549
Z315	プレート	91.419	113.184	1.651	150.9327
Z316	プレート	87.559	122.230	10.513	920.5077
				合計	-283.4386
				合計面積	141.71930
				地積	141.71 ㎡

地番	Ⓗ 250-95				
NO	境界標	Xn	Yn	Yn+1-Yn-1	Xn・(Yn+1-Yn-1)
Z315	プレート	91.419	113.184	16.301	1490.2211
Z313	プレート	103.550	120.579	-0.120	-12.4260
Z321	コンクリート杭	108.783	113.064	-8.911	-969.3653
C80	プレート	107.016	111.668	-2.158	-230.9405
Z311	金属鋲	107.570	110.906	-8.334	-896.4883
P17	プレート	98.068	103.334	-6.628	-649.9947
C82	プレート	95.219	104.278	9.850	937.9071
				合計	-331.0866
				合計面積	165.54330
				地積	165.54 ㎡

地番	Ⓘ 250-96				
NO	境界標	Xn	Yn	Yn+1-Yn-1	Xn・(Yn+1-Yn-1)
C80	プレート	107.016	111.668	2.158	230.9405
Z321	コンクリート杭	108.783	113.064	0.630	68.5332
P7	プレート	109.316	112.298	-2.158	-235.9039
Z311	金属鋲	107.570	110.906	-0.630	-67.7691
				合計	-4.1993
				合計面積	2.09965
				地積	2.09 ㎡

総合計面積	884.80805 ㎡

地番	Ⓐ 250-1	
公簿	合計面積	残地
967.86	884.80805	83.05195
	地積	83.05 ㎡

地番	面積
Ⓐ 250-1	83.05195 ㎡
Ⓑ 250-89	155.92045 ㎡
Ⓒ 250-90	127.68715 ㎡
Ⓓ 250-91	147.07970 ㎡
Ⓔ 250-92	5.02355 ㎡
Ⓕ 250-93	139.73495 ㎡
Ⓖ 250-94	141.71930 ㎡
Ⓗ 250-95	165.54330 ㎡
Ⓘ 250-96	2.09965 ㎡

平成 壱四年 壱〇月 弐壱日 登記

作製者	足柄上郡開成町吉田島[illegible]3 土地家屋調査士 石川 徹 (平成14年10月7日作製)

(神奈川県土地家屋調査士会)

申請人	松浦建設株式会社 代表取締役 松浦秀和	縮尺	1/

14.10.21