
地　　番	306-1，-3～-13
土地の所在	藤沢市西俣野字北窪

地　積　測　量　図

1/3

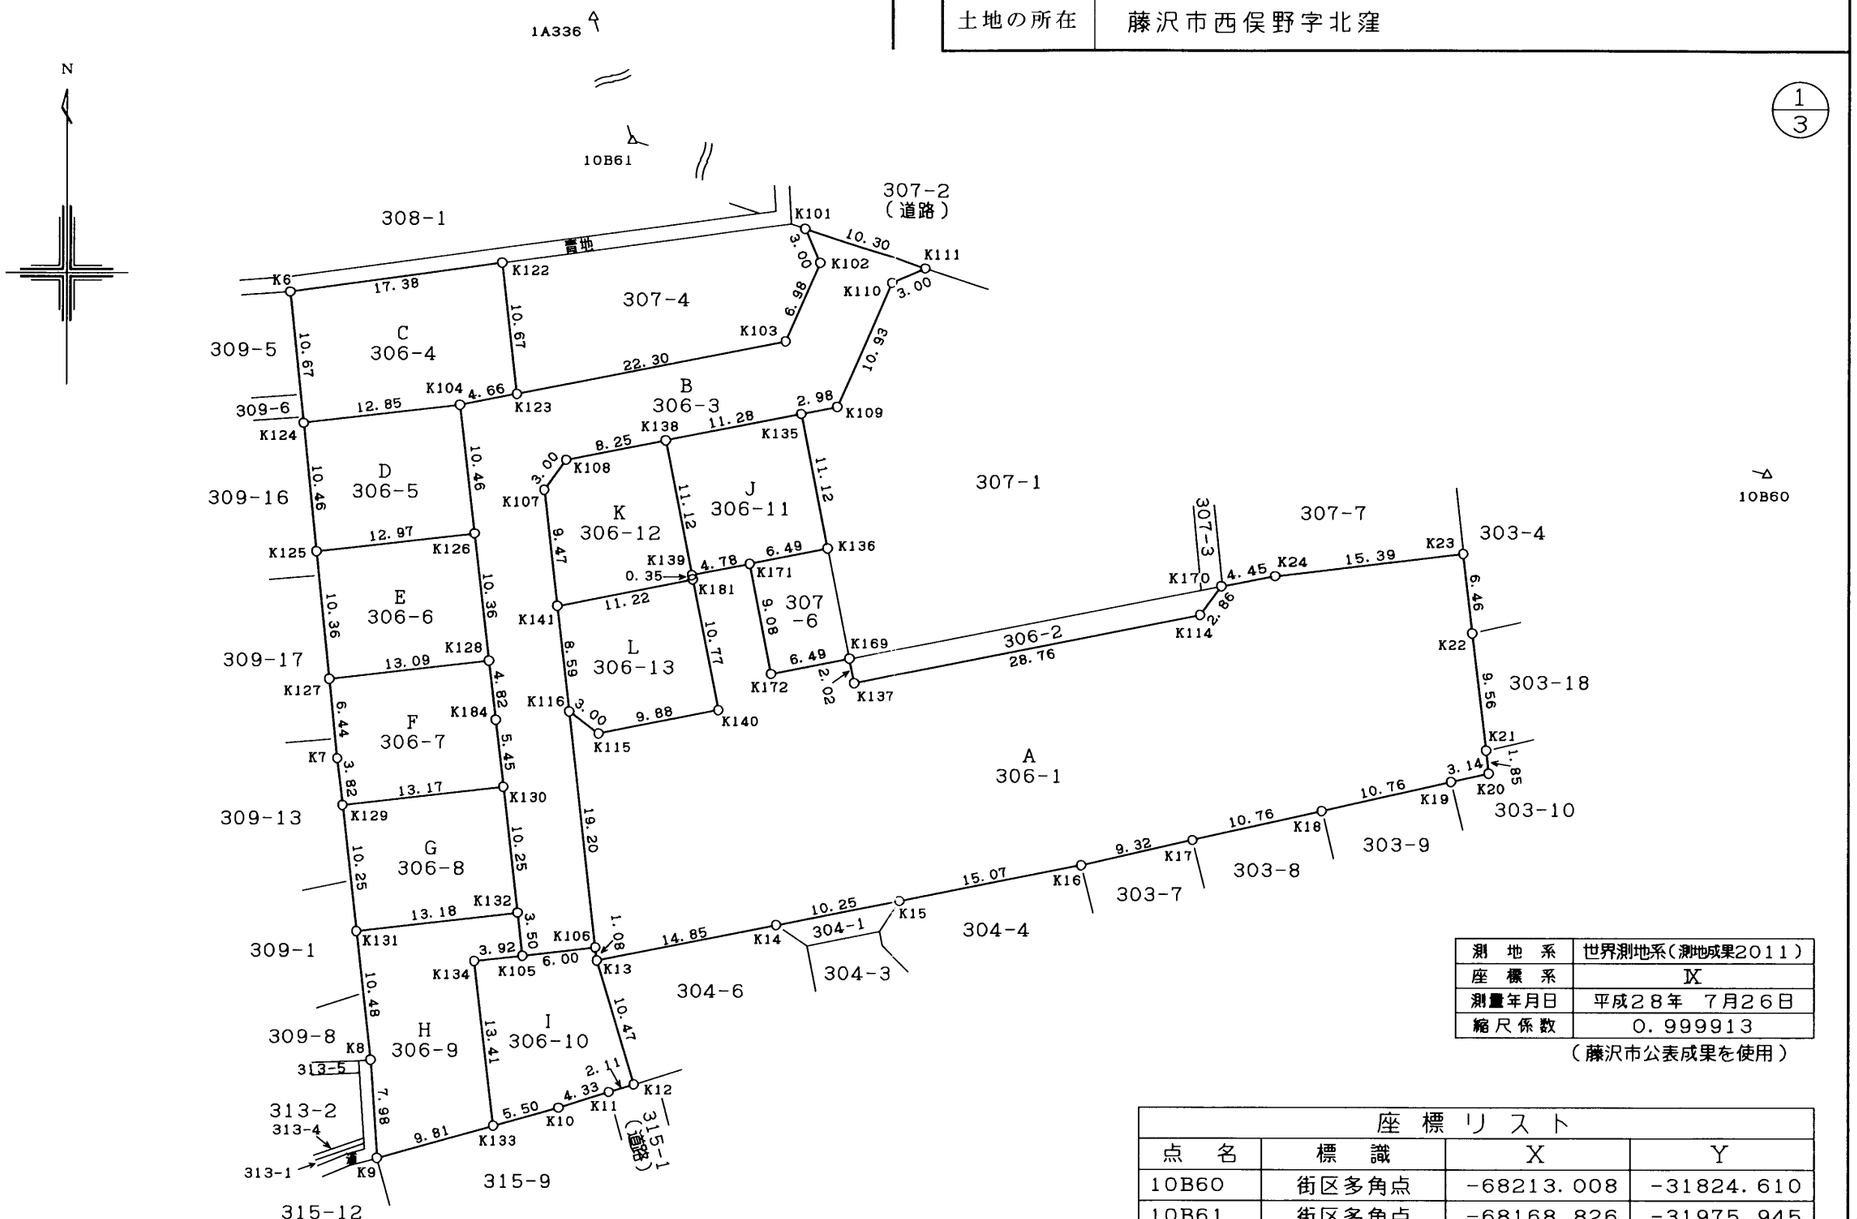

測　地　系	世界測地系（測地成果2011）
座　標　系	Ⅸ
測量年月日	平成２８年　７月２６日
縮尺係数	０．９９９９１３

（藤沢市公表成果を使用）

座　標　リ　ス　ト

点　名	標　識	X	Y
10B60	街区多角点	-68213.008	-31824.610
10B61	街区多角点	-68168.826	-31975.945
1A336	街区多角節点	-68109.226	-31994.758

作成者	藤沢市湘南台一丁目２０番地２３ 土地家屋調査士　小林　道雄　（平成29年12月 4日作成）	申請人	株式会社　一平不動産 代表取締役　廣木　正雄	縮尺	1／500

（長源納）

地番	306-1, -3~-13
土地の所在	藤沢市西俣野字北窪

地積測量図

座標求積表

地番	C 306-4				
筆界点	境界標	X	Y	$X_{n+1}-X_{n-1}$	$Y(X_{n+1}-X_{n-1})$
K122	図上点	-68195.972	-31927.705	8.260	-263722.843300
K6	市・コンクリート杭	-68198.316	-31944.929	-12.963	414102.114627
K124	図上点	-68208.935	-31943.839	-9.162	292669.452918
K104	図上点	-68207.478	-31931.071	2.359	
K123	図上点	-68206.576	-31926.495	11.506	-367346.251470
				倍面積	377.076286
				面積	188.538143
				地積	188.53 ㎡
				坪数	57.03

地番	D 306-5				
筆界点	境界標	X	Y	$X_{n+1}-X_{n-1}$	$Y(X_{n+1}-X_{n-1})$
K104	図上点	-68207.478	-31931.071	8.938	-285399.912598
K124	図上点	-68208.935	-31943.839	-11.867	379077.537413
K125	図上点	-68219.345	-31942.772	-8.938	285504.496136
K126	図上点	-68217.873	-31929.884	11.867	-378911.933428
				倍面積	270.187523
				面積	135.093761
				地積	135.09 ㎡
				坪数	40.86

地番	E 306-6				
筆界点	境界標	X	Y	$X_{n+1}-X_{n-1}$	$Y(X_{n+1}-X_{n-1})$
K126	図上点	-68217.873	-31929.884	8.826	-281813.156184
K125	図上点	-68219.345	-31942.772	-11.783	376381.682476
K127	図上点	-68229.656	-31941.714	-8.826	281917.567764
K128	図上点	-68228.171	-31928.708	11.783	-376215.966364
				倍面積	270.127692
				面積	135.063846
				地積	135.06 ㎡
				坪数	40.85

地番	F 306-7				
筆界点	境界標	X	Y	$X_{n+1}-X_{n-1}$	$Y(X_{n+1}-X_{n-1})$
K128	図上点	-68228.171	-31928.708	3.304	-105492.451232
K127	図上点	-68229.656	-31941.714	-7.901	252371.482314
K7	民・コンクリート杭	-68236.072	-31941.057	-10.221	326469.543597
K129	民・コンクリート杭	-68239.877	-31940.628	-2.311	73814.791308
K130	図上点	-68238.383	-31927.542	6.917	-220842.808014
K184	図上点	-68232.960	-31928.161	10.212	-326050.380132
				倍面積	270.177841
				面積	135.088920
				地積	135.08 ㎡
				坪数	40.86

座標求積表

地番	A 306-1				
筆界点	境界標	X	Y	$X_{n+1}-X_{n-1}$	$Y(X_{n+1}-X_{n-1})$
K23	民・プレート	-68219.464	-31849.404	4.621	-147176.095884
K24	図上点(印)	-68221.263	-31864.692	-2.634	83931.598728
K170	図上点	-68222.098	-31869.068	-3.142	100132.611656
K114	図上点	-68224.405	-31870.774	-7.866	250695.508284
K137	図上点	-68229.964	-31899.000	-3.576	114070.824000
K169	図上点	-68227.981	-31899.390	0.745	-23765.045550
K172	図上点	-68229.219	-31905.767	7.678	-244972.479026
K171	図上点	-68220.303	-31907.523	7.992	-255004.923816
K139	図上点	-68221.227	-31912.219	-1.273	40624.254787
K181	図上点	-68221.576	-31912.150	-10.918	348416.853700
K140	図上点	-68232.145	-31910.068	-12.479	398205.738572
K115	図上点	-68234.055	-31919.764	-0.136	4341.087904
K116	図上点	-68232.281	-31922.191	-17.310	552573.126210
K106	図上点	-68251.365	-31920.013	-20.160	643507.462080
K13	民・コンクリート杭	-68252.441	-31919.891	1.795	-57296.204345
K14	民・コンクリート杭	-68249.570	-31905.321	4.853	-154836.522813
K15	民・コンクリート杭	-68247.588	-31895.259	4.894	-156095.397546
K16	民・コンクリート杭	-68244.676	-31880.473	4.957	-158031.504661
K17	民・プレート	-68242.631	-31871.370	4.403	-140329.642110
K18	民・プレート	-68240.273	-31860.868	4.717	-150287.714356
K19	民・プレート	-68237.914	-31850.369	3.047	-97048.074343
K20	民・プレート	-68237.226	-31847.305	2.529	-80541.834345
K21	民・プレート	-68235.385	-31847.522	11.342	-361214.594524
K22	民・プレート	-68225.884	-31848.645	15.921	-507062.277045
				倍面積	2836.755557
				面積	1418.377778
				地積	1418.37 ㎡
				坪数	429.05

地番	B 306-3				
筆界点	境界標	X	Y	$X_{n+1}-X_{n-1}$	$Y(X_{n+1}-X_{n-1})$
K101	図上点	-68193.137	-31903.009	0.445	-14196.839005
K102	図上点	-68195.881	-31901.784	-9.128	291199.484352
K103	図上点	-68202.265	-31904.607	-11.597	369997.727379
K104	図上点	-68207.478	-31931.071	-30.695	980124.224345
K184	図上点	-68232.960	-31928.161	-44.569	1423006.207609
K105	図上点	-68252.047	-31925.982	-18.405	587597.698710
K106	図上点	-68251.365	-31920.013	19.766	-630930.976958
K116	図上点	-68232.281	-31922.191	37.032	-1182142.577112
K107	図上点	-68214.333	-31924.241	20.375	-650456.410375
K108	図上点	-68211.906	-31922.466	6.777	-216338.552082
K109	図上点	-68207.556	-31900.377	14.354	-457898.011458
K110	図上点	-68197.552	-31895.953	11.230	-358191.552190
K111	図上点	-68196.326	-31893.211	4.415	-140808.526565
				倍面積	961.896650
				面積	480.948325
				地積	480.94 ㎡
				坪数	145.48

（長源納）

作成者	藤沢市湘南台一丁目20番地の3 土地家屋調査士 小林 道雄	（平成29年12月 4日作成）

申請人	株式会社 一平不動産 代表取締役 廣木 正雄	縮尺	1／

表示年月日：2026／08／27

地番	306-1，-3～-13
土地の所在	藤沢市西俣野字北窪

地積測量図

座標求積表

地番	K 306-12				
筆界点	境界標	X	Y	$X_{n+1}-X_{n-1}$	$Y(X_{n+1}-X_{n-1})$
K138	図上点	-68210.311	-31914.370	9.321	-297473.842770
K108	図上点	-68211.906	-31922.466	-4.022	128392.158252
K107	図上点	-68214.333	-31924.241	-11.838	377919.164958
K141	図上点	-68223.744	-31923.166	-7.243	231219.491338
K181	図上点	-68221.576	-31912.150	2.517	-80322.881550
K139	図上点	-68221.227	-31912.219	11.265	-359491.147035
				倍面積	242.943193
				面積	121.471596
				地積	121.47 ㎡
				坪数	36.74

地番	L 306-13				
筆界点	境界標	X	Y	$X_{n+1}-X_{n-1}$	$Y(X_{n+1}-X_{n-1})$
K181	図上点	-68221.576	-31912.150	8.401	-268093.972150
K141	図上点	-68223.744	-31923.166	-10.705	341737.492030
K116	図上点	-68232.281	-31922.191	-10.311	329149.711401
K115	図上点	-68234.055	-31919.764	0.136	-4341.087904
K140	図上点	-68232.145	-31910.068	12.479	-398205.738572
				倍面積	246.404805
				面積	123.202402
				地積	123.20 ㎡
				坪数	37.26

合計	3312.61	㎡

座標求積表

地番	G 306-8				
筆界点	境界標	X	Y	$X_{n+1}-X_{n-1}$	$Y(X_{n+1}-X_{n-1})$
K130	図上点	-68238.383	-31927.542	8.690	-277450.339980
K129	民・コンクリート杭	-68239.877	-31940.628	-11.680	373066.535040
K131	民・コンクリート杭	-68250.063	-31939.483	-8.690	277554.107270
K132	図上点	-68248.567	-31926.379	11.680	-372900.106720
				倍面積	270.195610
				面積	135.097805
				地積	135.09 ㎡
				坪数	40.86

地番	H 306-9				
筆界点	境界標	X	Y	$X_{n+1}-X_{n-1}$	$Y(X_{n+1}-X_{n-1})$
K132	図上点	-68248.567	-31926.379	1.984	-63341.935936
K131	民・コンクリート杭	-68250.063	-31939.483	-11.916	380590.879428
K8	市・コンクリート杭	-68260.483	-31938.311	-18.385	587185.847735
K9	市・プレート	-68268.448	-31937.808	-5.342	170611.770336
K133	図上点	-68265.825	-31928.355	15.956	-509448.832380
K134	図上点	-68252.492	-31929.877	13.778	-439929.845306
K105	図上点	-68252.047	-31925.982	3.925	-125309.479350
				倍面積	358.404527
				面積	179.202263
				地積	179.20 ㎡
				坪数	54.20

地番	I 309-10				
筆界点	境界標	X	Y	$X_{n+1}-X_{n-1}$	$Y(X_{n+1}-X_{n-1})$
K106	図上点	-68251.365	-31920.013	0.394	-12576.485122
K105	図上点	-68252.047	-31925.982	-1.127	35980.581714
K134	図上点	-68252.492	-31929.877	-13.778	439929.845306
K133	図上点	-68265.825	-31928.355	-11.862	378734.147010
K10	民・コンクリート杭	-68264.354	-31923.054	2.736	-87341.475744
K11	市・コンクリート杭	-68263.089	-31918.909	1.882	-60071.386738
K12	民・コンクリート杭	-68262.472	-31916.884	10.648	-339850.980832
K13	民・コンクリート杭	-68252.441	-31919.891	11.107	-354534.229337
				倍面積	270.016257
				面積	135.008128
				地積	135.00 ㎡
				坪数	40.83

地番	J 306-11				
筆界点	境界標	X	Y	$X_{n+1}-X_{n-1}$	$Y(X_{n+1}-X_{n-1})$
K135	図上点	-68208.131	-31903.301	8.737	-278739.140837
K138	図上点	-68210.311	-31914.370	-13.096	417950.589520
K139	図上点	-68221.227	-31912.219	-9.992	318866.892248
K171	図上点	-68220.303	-31907.523	2.179	-69526.492617
K136	図上点	-68219.048	-31901.150	12.172	-388300.797800
				倍面積	251.050514
				面積	125.525257
				地積	125.52 ㎡
				坪数	37.97

（長源納）

作成者	藤沢市湘南台一丁目20番地の2 土地家屋調査士 小林 道雄	（平成29年12月 4日作成）

申請人	株式会社 一平不動産 代表取締役 廣木 正雄	縮尺	1／