
参考図(城山4丁目20-18付近) 縮尺 1/250

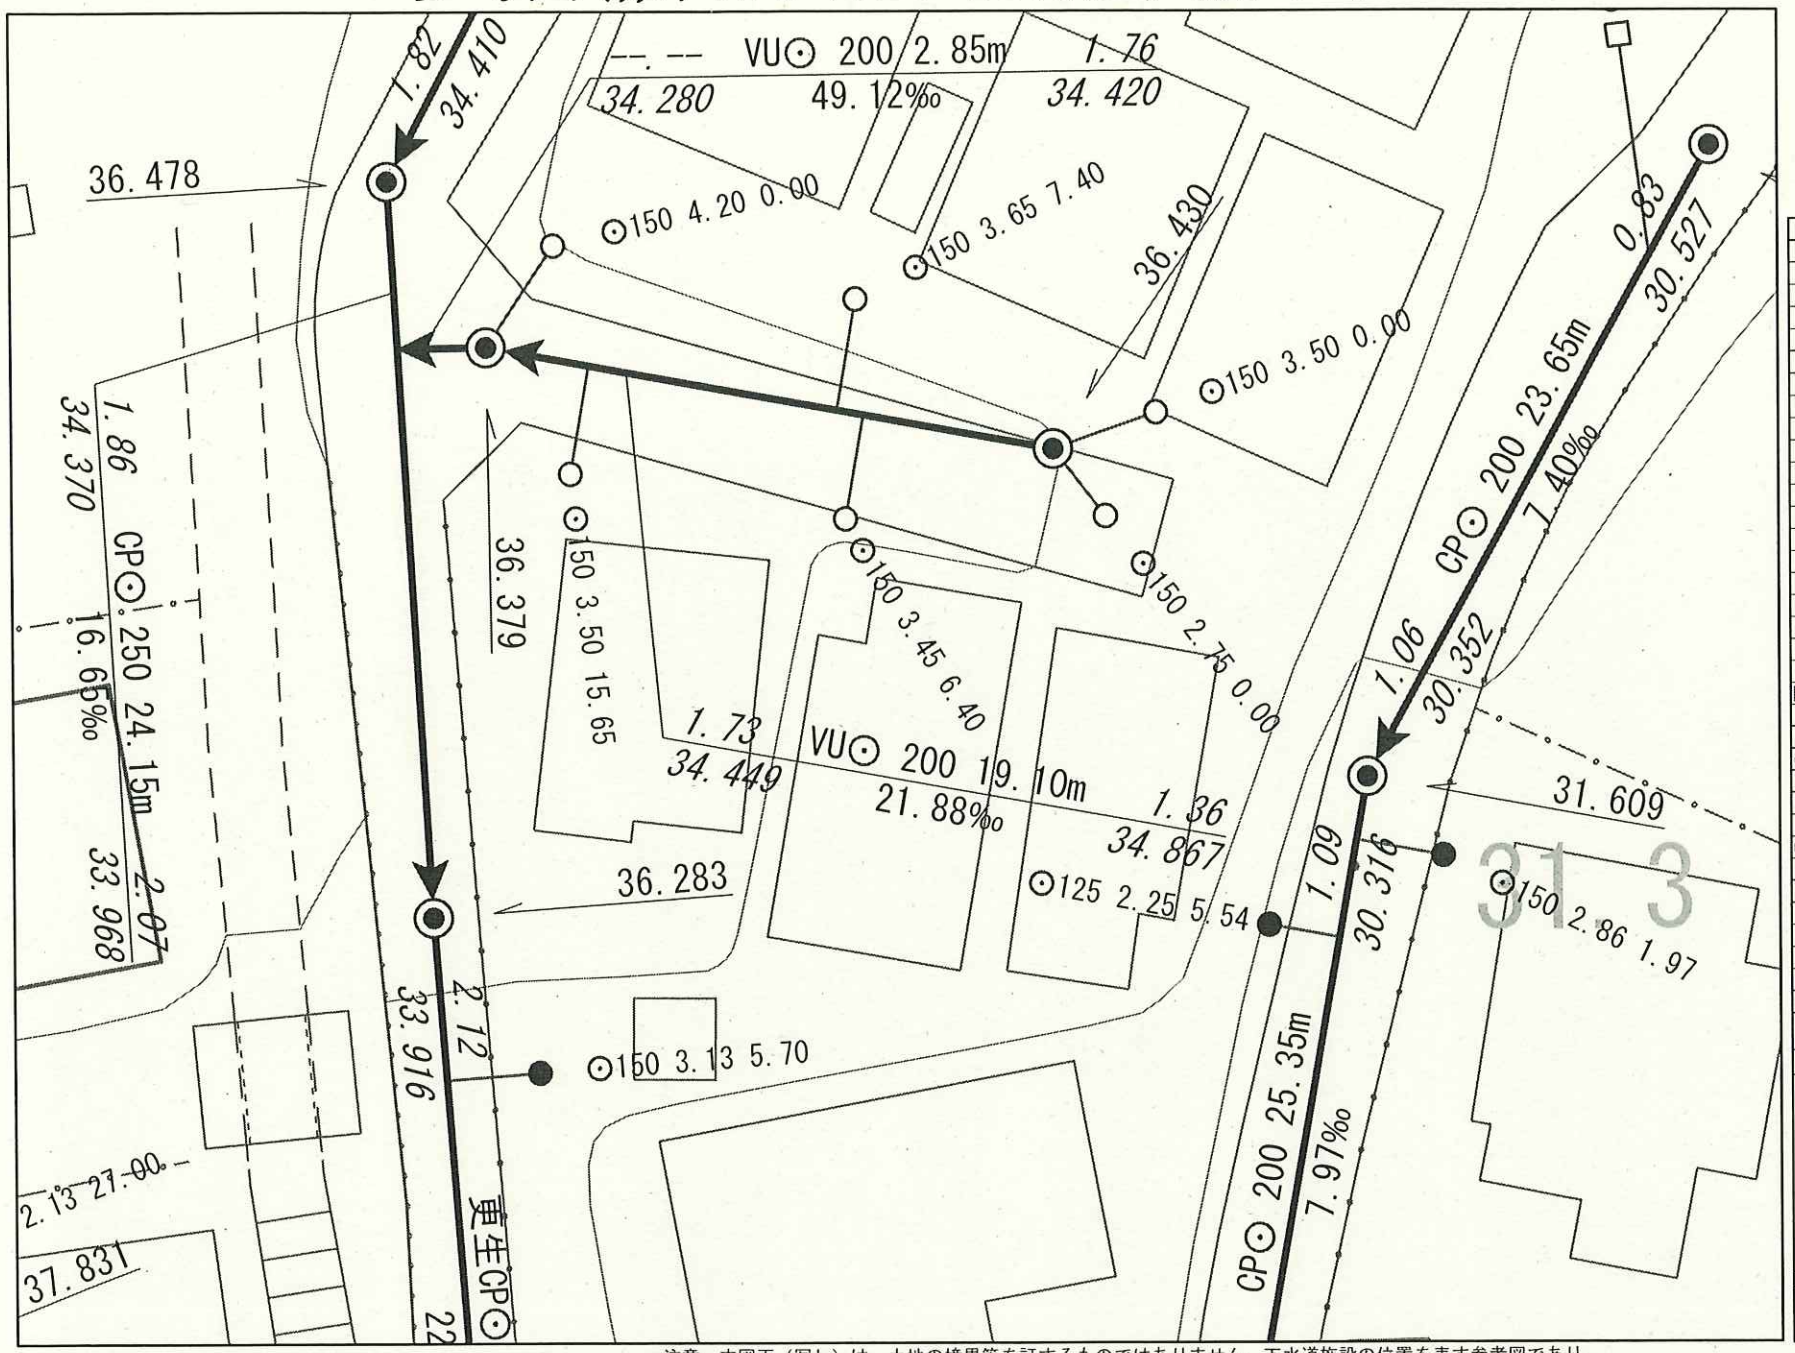

凡例

管渠	
	流域幹線
	幹線管渠
	枝線管渠
	圧送管

人孔			
◉	1号人孔	⊠	伏越人孔
◎	2号人孔	⊡	副室人孔
◍	3号人孔	◉	特1号人孔
◍	4号人孔	◎	特2号人孔
○	斜人孔	◍	特3号人孔
△	Y号人孔	◍	特4号人孔
▲	0号人孔	XX	特殊人孔(形状不明)
⬭	楕円人孔	P	ポンプ場
⊠	特殊人孔(角形 type-A)	●	点検孔(円形)
⊠	特殊人孔(角形 type-B)	■	点検孔(矩形)
○	特殊人孔(円形)	▨	点検孔(グレーチング)
□	特殊人孔(角形)	△	吐け口
㊦	塩ビ小口径人孔	—	キャップ止め
㊦	レジン小口径人孔	T	処理場
5 ～ 6	5号～6号人孔	⑭	不明
7	7号人孔		

中継ポンプ			
㊱ ～ ㊲	マンホールポンプ0号～7号人孔		

管種			
VU	硬質塩化ビニル管(外肉管)	CP	陶管
HP	遠心力鉄筋コンクリート管(ヒューム管)	VP	硬質塩化ビニル管(厚肉)
PRP	リブ付硬質塩化ビニル管	VPH	高耐性塩化ビニル管
VE	硬質塩化ビニル管(異形管)	VEH	高耐性異形管

ます			
●	コンクリートφ40	□	コンクリート角形
■	コンクリートφ30×30	✕	側溝去
⊠	コンクリートφ36×36	—	キャップ止め
○	塩ビ製	⑭	不明

人孔属性

1.366 地盤高

管渠属性

更生有無 管材質 管断面 呼び径 区間延長
下流管渠深 上流管渠深
2.69 更生HP○ 250 39.40m 2.53
6.557 4.97‰ 6.708
下流管底高 勾配 上流管底高

取付管属性

管断面 呼び径
○100 1.64 18.98
取付管延長 上位人孔からの距離

1/250

0m 5m 10m 15m 20m

注意　本図面（写し）は、土地の境界等を証するものではありません。下水道施設の位置を表す参考図であり、必ずしも実際と一致するものではありません。工事等における下水道施設の位置の確認については、必ず手掘による試験掘を行ってください。（公道上を掘削する場合は道路管理者の許可を得ること）
また、下水道施設の確認以外の目的に本図面を使用する事を禁じます。

小田原市

令和７年５月９日

参考図

このシステムの情報は、水道施設の維持管理に必要な精度で作成されているため、水道管が道路や家形とずれが生じる場合があります。

工事設計や土地取引などの資料に利用される場合は、水道管や水道メーターの位置を現地で十分調査してください。

なお、ご不明な点につきましては、必ず窓口にてお問い合わせください。

小田原市上下水道局

